01

概念设计：The 3E Stitcher

韧性催化剂：裕固族的3E缝合器

2025.10

合作项目

地点：甘肃皇城镇

总建筑面积：2257㎡

类型：UIA竞赛概念设计


竞赛主题与目标：

参与者被邀请围绕“韧性的催化剂”主题，自选场地，关注未来面临居住不便、不平等或崩溃风险的脆弱地区。竞赛呼吁空间干预，支持抵抗和适应政治变革、社会转型和气候变化带来的可预见威胁。提案应探讨如何通过利用时间作为设计工具来培养韧性。

自选场地与目标：

皇城镇位于甘肃省南部，是裕固族唯一的聚居地。居民主要从事农业和畜牧业牧场位于南部地区。该地区适合饲养长手羊，拥右美丽的自然环境，具有发展手工艺和旅游的潜力。

但是目前生态、经济与民族危机三个方面的危机，我们想提供概念设计去解决裕固族面临的危机。

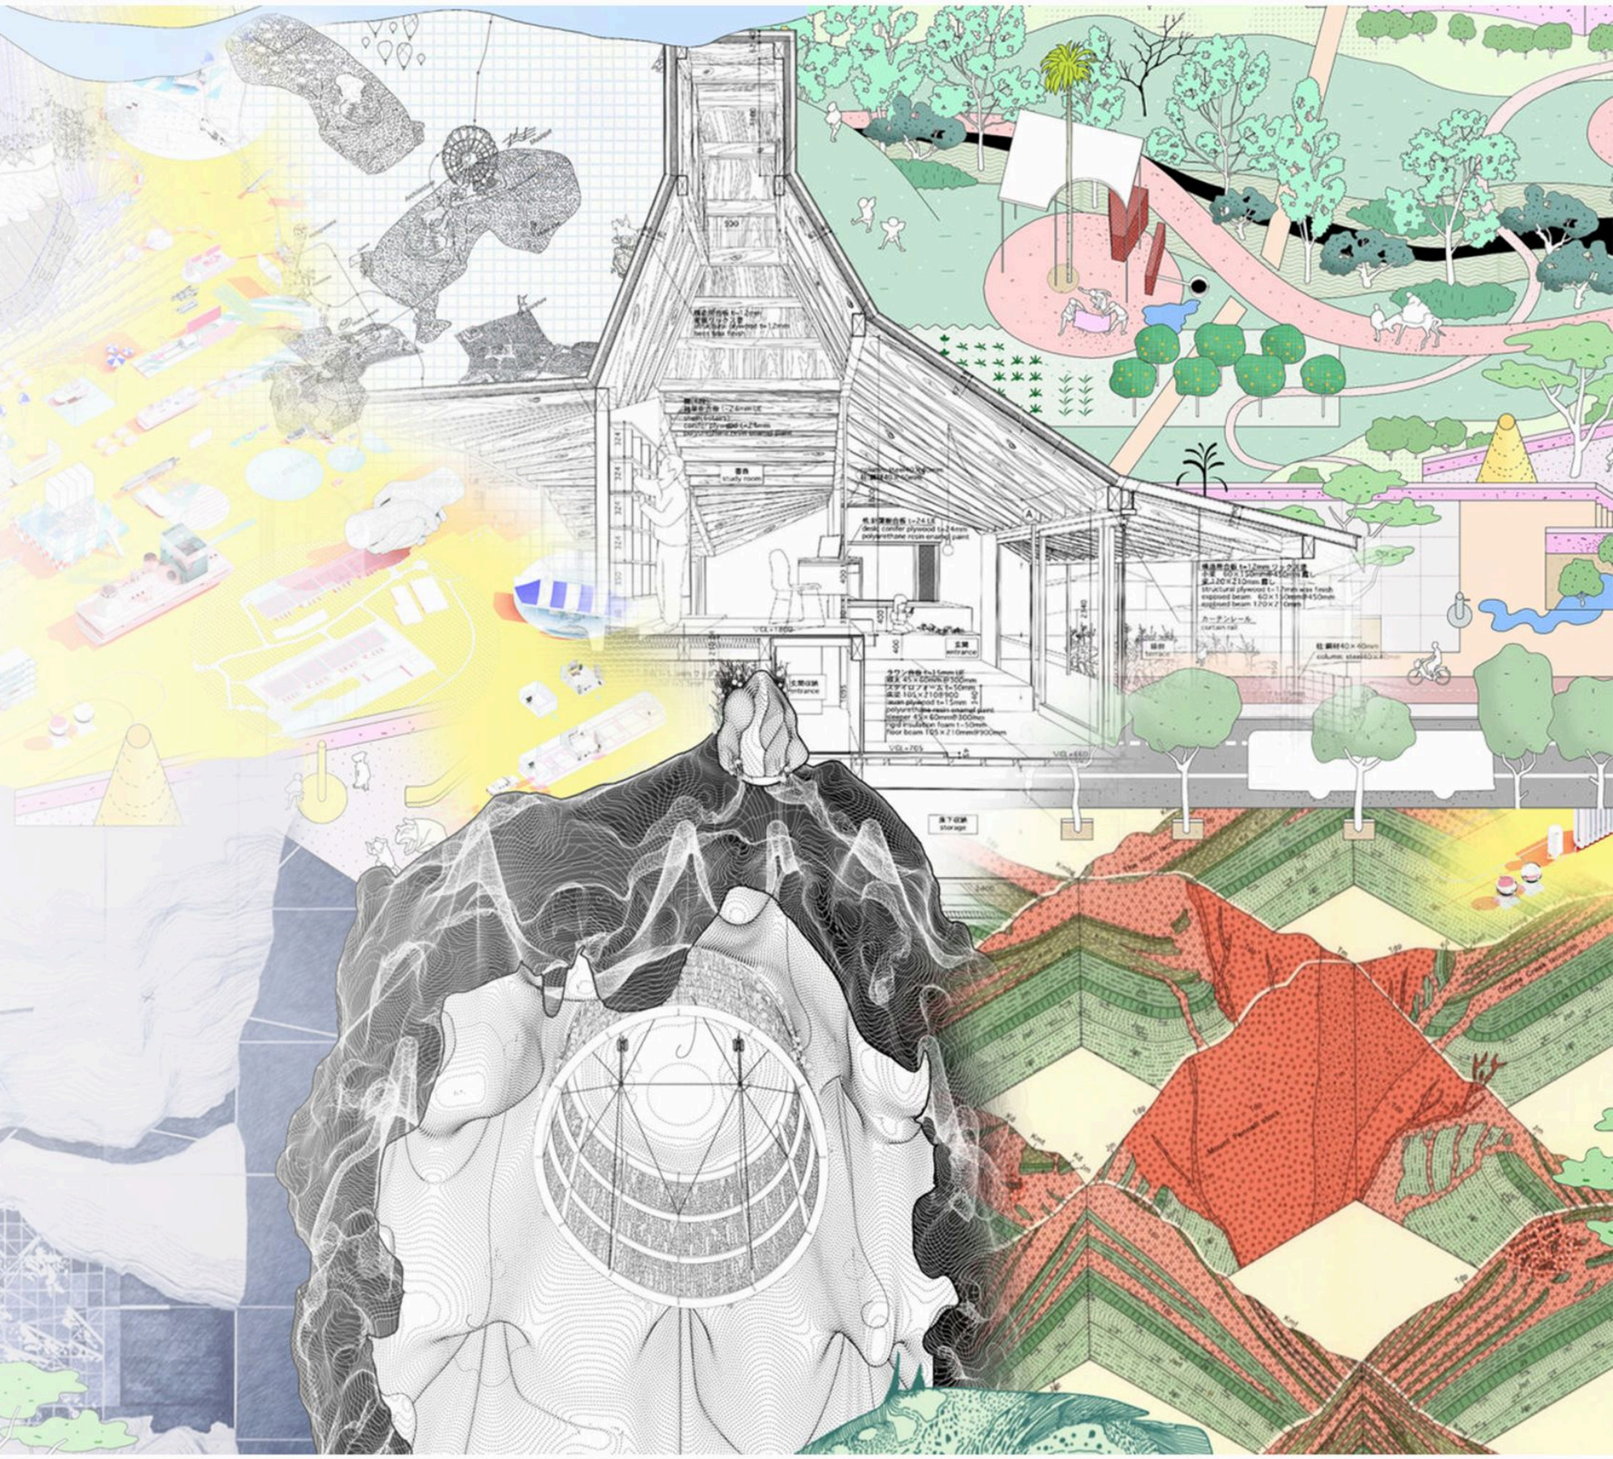

68f5d2387bf52

The 3E Stitcher

In what ways does the Yugur ethnic group exist?


Huangcheng Town is located in the south of Gansu Province and is theonly settlement of the **Yugur ethnic group**. The residents mainly engage in agriculture and animal husbandry, with the grazing area located in the south.

This area is suitable for raising **long-haired sheep** and has a **beautiful natural environment**, Has **the potential to develop handicrafts and tourism**. but these resources have not been valued.



Economic issues

The industrial structure is single-focused, mainly based on agriculture and animal husbandry, with short industrial chains and insufficient deep processing. There is an outflow of young labor and a lack of professional talents.

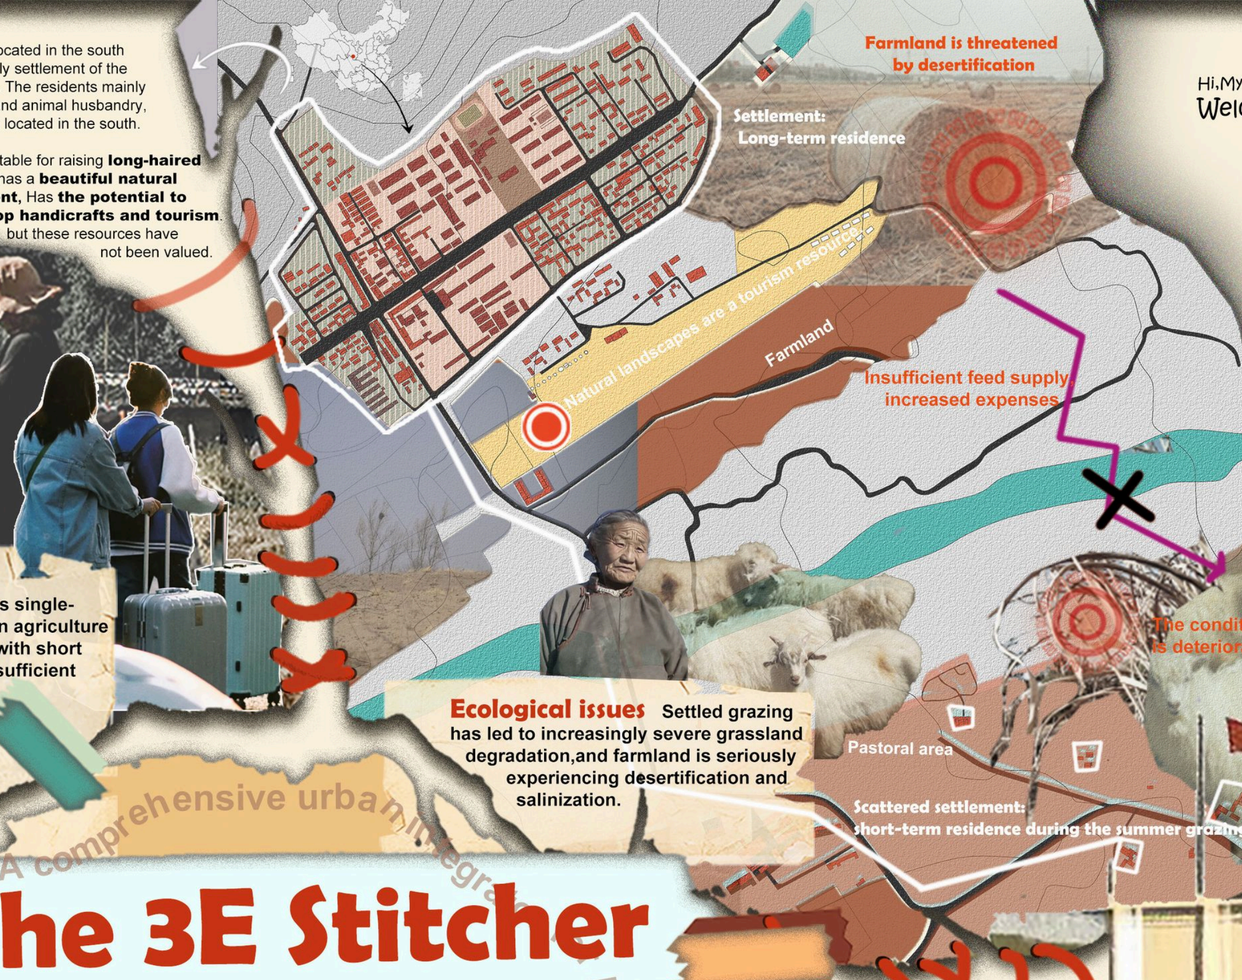

Ecological issues

Settled grazing has led to increasingly severe grassland degradation,and farmland is seriously experiencing desertification and salinization.

Hi,My name is Sai Ji.

Welcome to listen to my story!

I'm in the second grade of primary school and I study at the only school in the town. Today, we didn't have music class again. The teacher said that the school is short of music teachers and we'll have it once every two weeks.

When I got home, my mother was working in the fields and my father was working in the town during the grazing break to earn money. Due to the drought, the cost of feed has increased. My father said he would have to work harder to support the family.

After feeding the cattle and sheep, I made myself something to eat and started doing my homework.

My mother said that if I studied hard, I could leave here and have a better life...

2025.11.01

A comprehensive urban integrated ... Ecology, Economy, and Ethnicity. A Comprehensive ...

Eighty years ago,

the Yugur people led a nomadic life following water and grass.
Their lives were enriched by their colorful ethnic costumes, grand wedding scenes, large-scale sacrificial ceremonies and knowledge passed down orally.



Ethnic crisis


After settling down, the form of collective living no longer exists, ethnic customs and traditions are gradually forgotten by the younger generation, and national culture is disappearing.



Large-scale ethnic events are no longer common, but small-scale ritual activities are frequently conducted.


Since 1950,

influenced by national policies, the Yugur people have begun a settled life. Every summer, they go to their fixed pastures to graze their livestock. To supplement their income, many families have started to engage in agriculture.

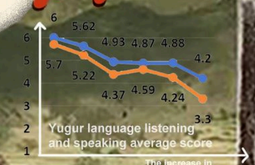

Nowadays,

the heavy burden of agriculture and animal husbandry not only reduces their available time for activities, but also the distance between the pastoral areas and the settlements further hinders family reunions.
Moreover, ethnic activities have gradually faded away.

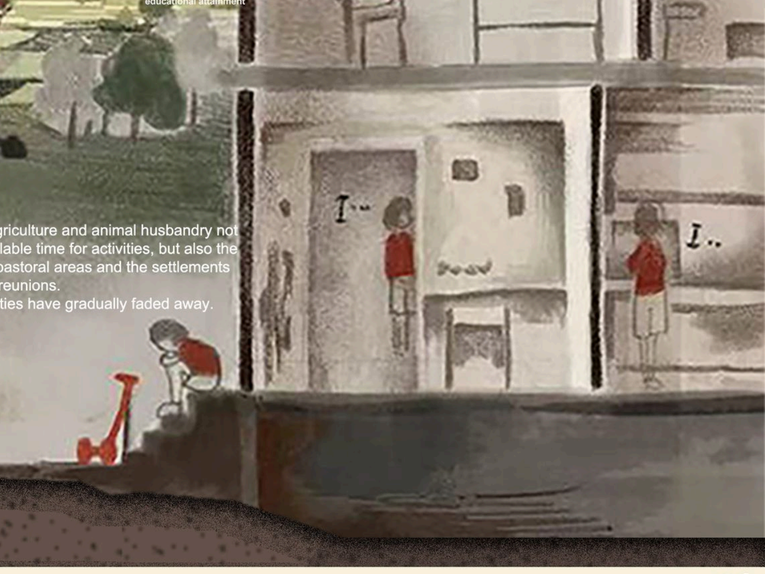

Summary of Issues → mode of expression → Demand for catalysts → measures → target

Ecology — Raw materials → Production → Sustainable production methods


Economy — Product → market → Efficient sales method

Ethnicity — Funds → livelihood → A conscious lifestyle

National spirit

The 3E Stitcher


Design a device to promote the development of ecology, economy and Ethnicity, thereby strengthening the kinship among the Yugur people, preserving their ethnic culture and fostering their national spirit.

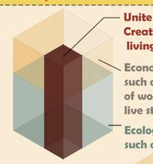

Unite the national spirit:, Create distinctive national living spaces.

Economic development, such as the production of wool products and online live streaming sales.

Ecological protection, such as vertical farming.

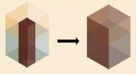
Time strategy: 

Corner spaces of residential courtyards, areas near livestock pens, and rooftops become potential site selections.


Family: Vertical Farm, Handicraft Workshop → Neighborhood: ethnic cuisine, homestays, folk experiences → Society: Regional vitality drives cultural revitalization and inheritance

Wool resources · Traditional nomadic building skills · Existing tourism resources as potential

STEP1:life mending (2027) → STEP2:community integration (2028) → STEP3:spiritual generator (2040)

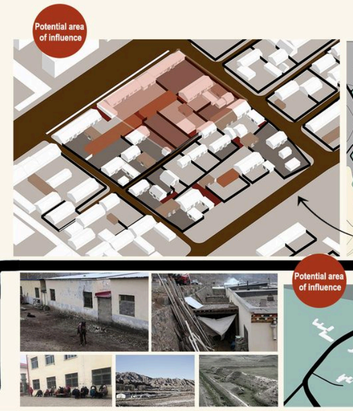

Step1: life mending ——Utilizing the corner and edge spaces to enhance efficiency for families

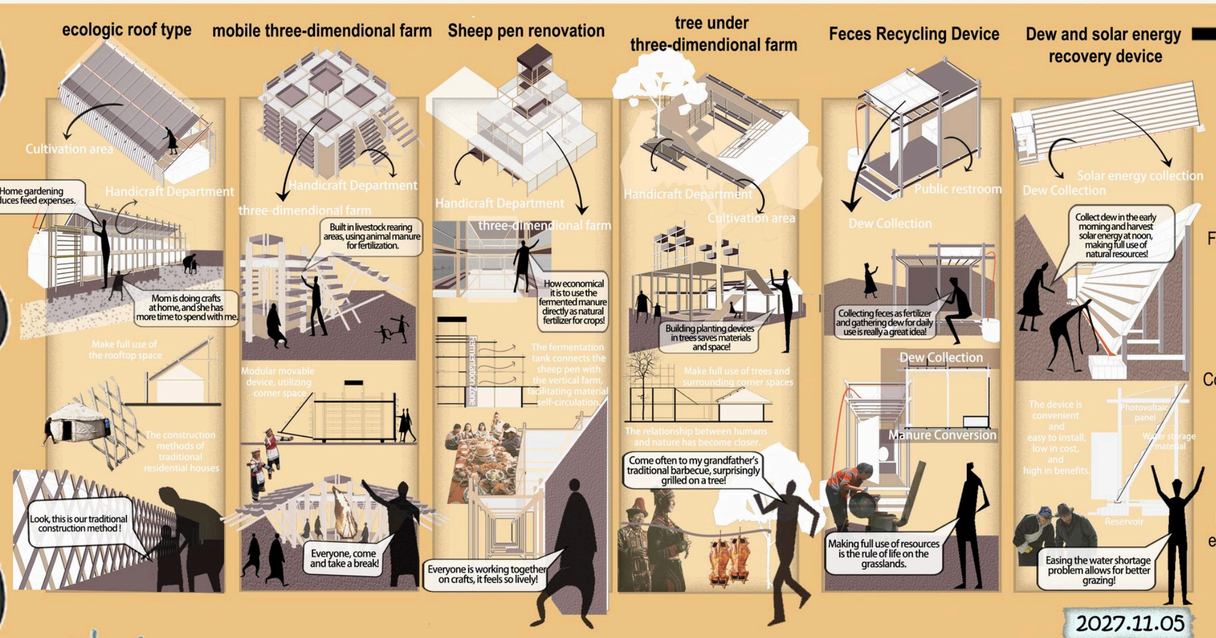

Function

Construct

Ethnic elements


2027.11.05


Mom said that with the government's suggestion and support, she wants to convert the roof and sheepfold of her home into a "vertical farm" plus a handicraft workshop. This can reduce some feed expenses, conserve the grassland, and also sell wool handicrafts through live streaming...

More families have built "farm towers". We often shout to the distance from the towers and listen to grandmothers singing folk songs on them...

Soon, a video of grandmothers singing on the tower in ethnic costumes went viral. More people got to know our ethnic group. They bought our woolen products to support us, and more people came to travel...

Step2: community integration——Expanding the market through the integration of culture and tourism

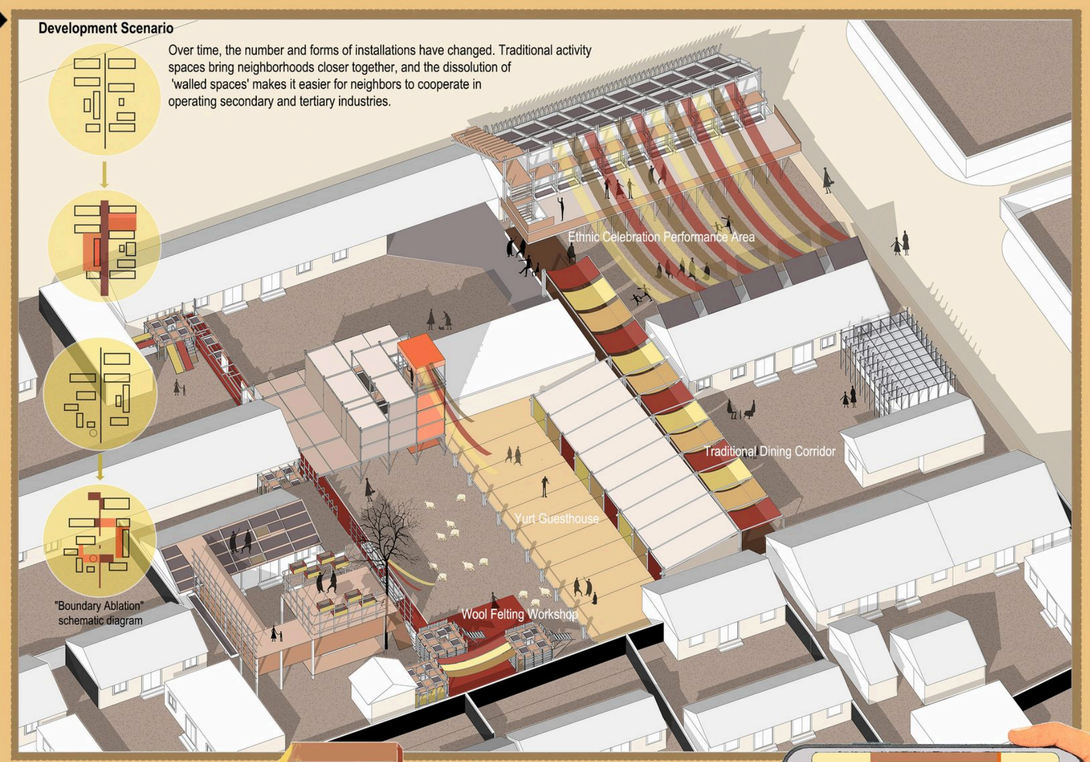

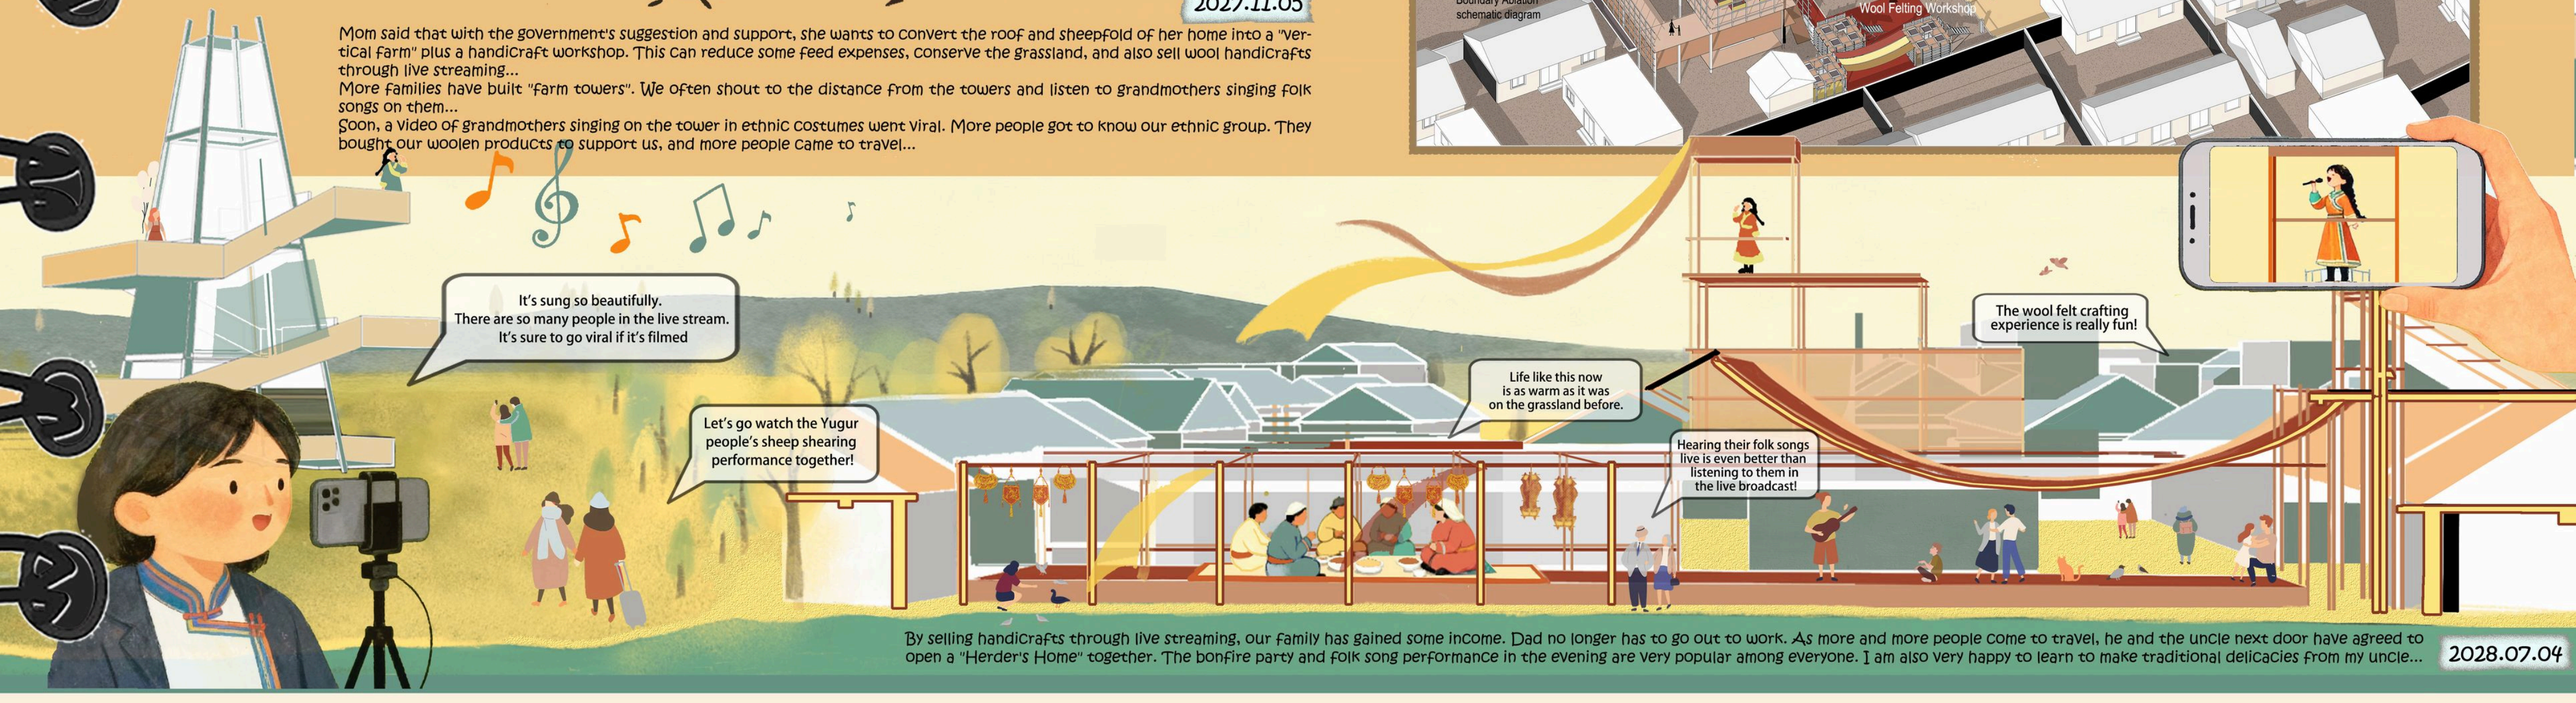

By selling handicrafts through live streaming, our family has gained some income. Dad no longer has to go out to work. As more and more people come to travel, he and the uncle next door have agreed to open a "Herder's Home" together. The bonfire party and folk song performance in the evening are very popular among everyone. I am also very happy to learn to make traditional delicacies from my uncle...

2028.07.04

Step3: spiritual generator ——Spiritual cohesion ensures the everlasting life of the nation.

This is what the ethnic culture of the Yugur people is really like!I didn't know before.

Whenever the lights come on, I seem to feel the warmth of the bonfire on the grassland.

My grandson especially likes this cultural corridor and has remembered several historical stories of the Yugur people!

2040.05.08

After graduating from university, the strong national spirit of my hometown deeply attracted me. I chose to return to my hometown. Many classmates in our town made the same choice as me. Some became environmentalists, and some became researchers of ethnic languages...

And I became a teacher. I proposed to offer courses such as ethnic history in the curriculum. In terms of revitalizing and inheriting the culture of the Yugur ethnic group, my classmates and I are working together...

Oral Tradition Education Space:
Study content: folk songs, Yugur language, cloud watching and weather prediction, animal husbandry knowledge, Yugur history...

The 'Cultural Corridor':
Exhibition of national culture and history, research points on national culture.

The collective lifestyle of neighborhood cooperation makes people feel warm and comfortable.

The spirit of the Yugur people inspires me, and when I grow up, I want to contribute to my hometown!

The development of the economy, ecology, and tourism has given the local residents a growing sense of ethnic identity...

Lighthouse User Manual:
During **large festivals**, everyone lights up their lamps;
when a family **gets married**, neighbors along the road will light their lamps;
when a family **slaughters a sheep**, they can invite everyone to share through the lights
.....
The collective and free time on the grasslands seems to have returned.


It's been a long time since everyone celebrated the sacrificial festival with such grandeur.

The ethnic song sung by the children is really beautiful!

02

单体设计：廊院阅垣

城墙脚下的回廊民宿:传统格局与现代生活的叠合

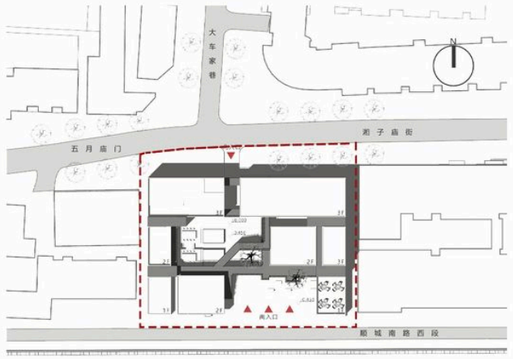



2025.01


个人项目


地点：西安明城区顺城巷南段

总建筑面积：2257㎡

类型：城市民宿建筑设计


项目毗邻西安古城墙，地处湘子庙与老旧社区环绕的传统街巷，同时叠加近年兴起的酒吧、餐厅等商业活力，形成新旧共生的独特场域。设计以“廊院”为概念，引入传统回字形布局，通过三级阶梯式退台体量呼应城墙的厚重轮廓，建筑向外舒展的姿态既强化了街道界面，也形成对历史文脉的谦和应答。内部回廊贯通二、三层，增强空间流动感；屋顶平台释放为公共活动场所，促进住客交往；底层沿街设置商铺，使民宿功能与城市生活自然接续。整体策略在保留历史气息的同时，注入当代使用需求，营造一个开放、互动且具有社区归属感的城市民宿。

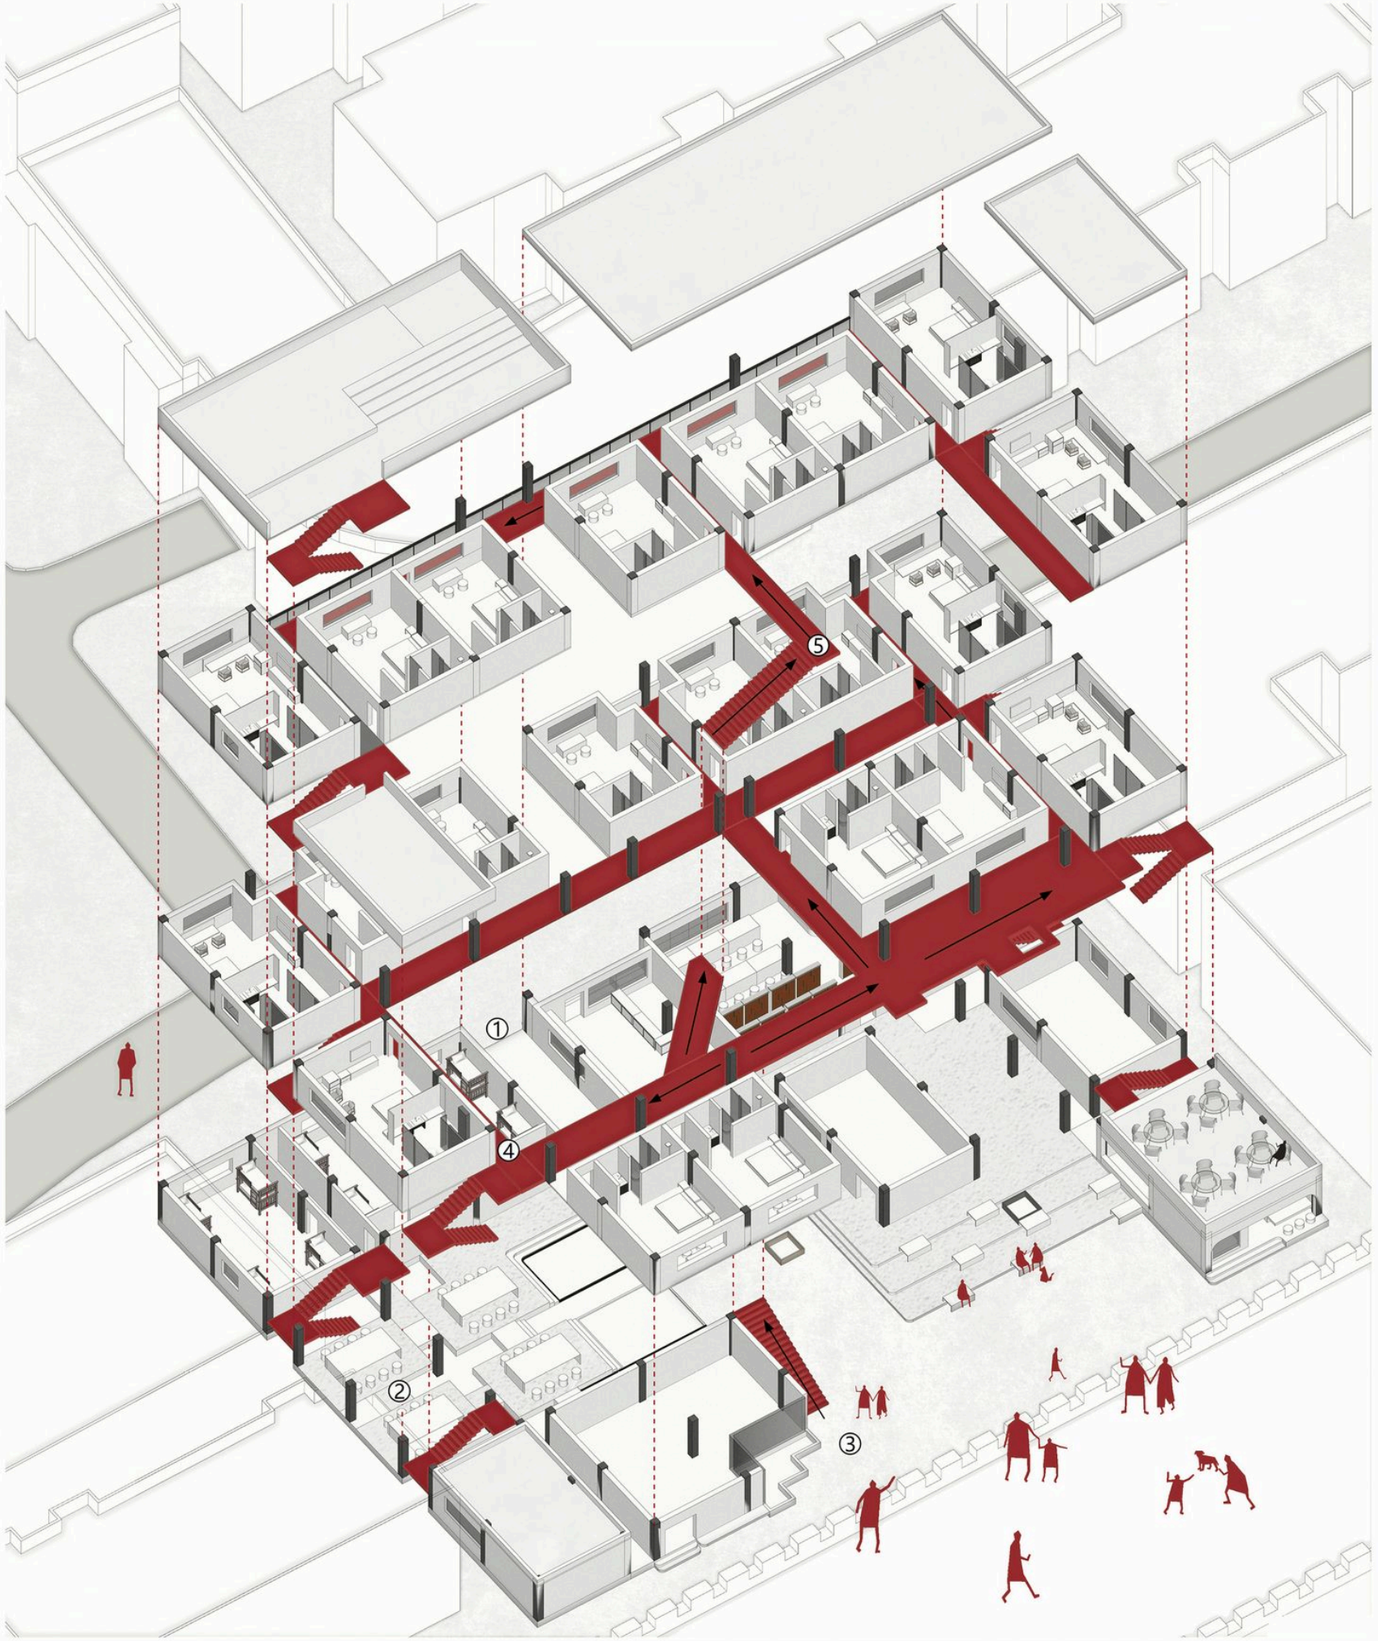


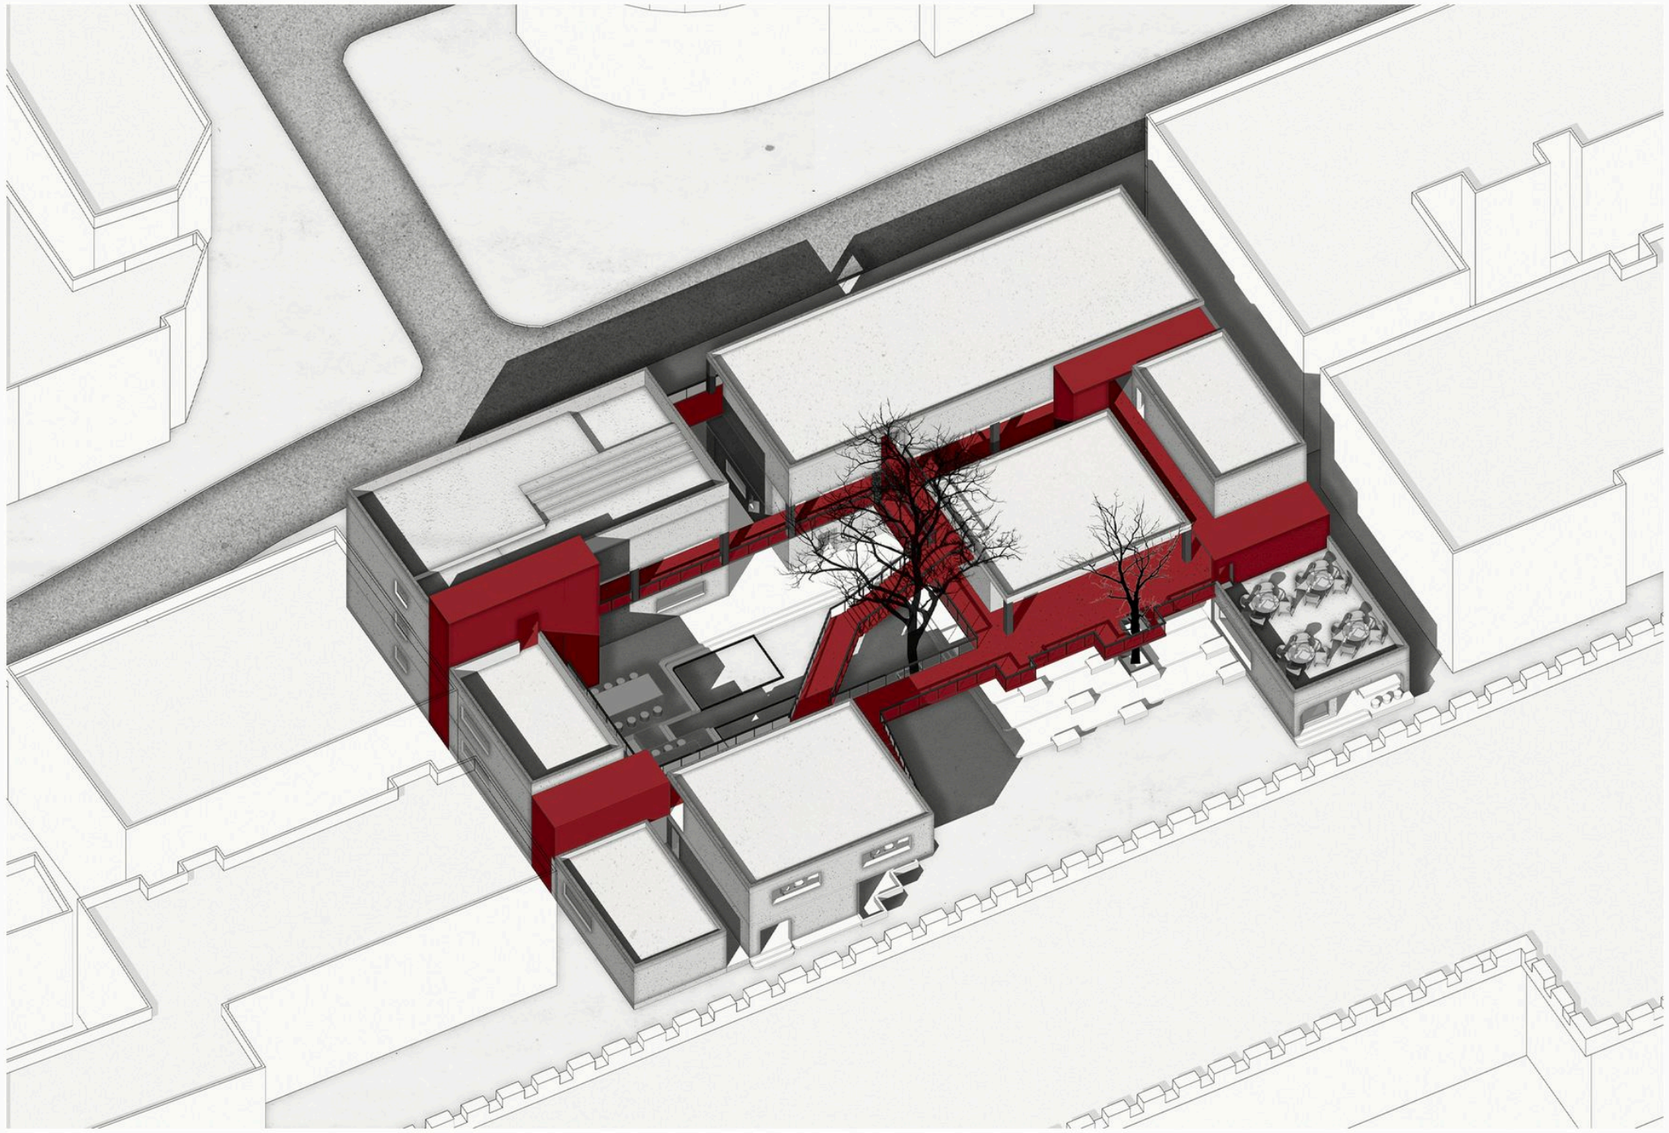


体量生成


挖空院落

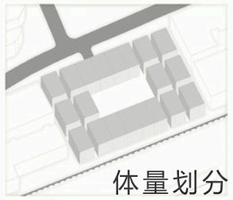
体量划分

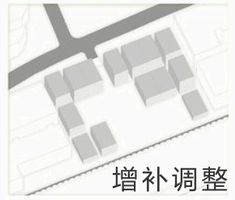
增补调整


水平链接



细节调整


A-A剖面图


B-B剖面图


C-C剖面图



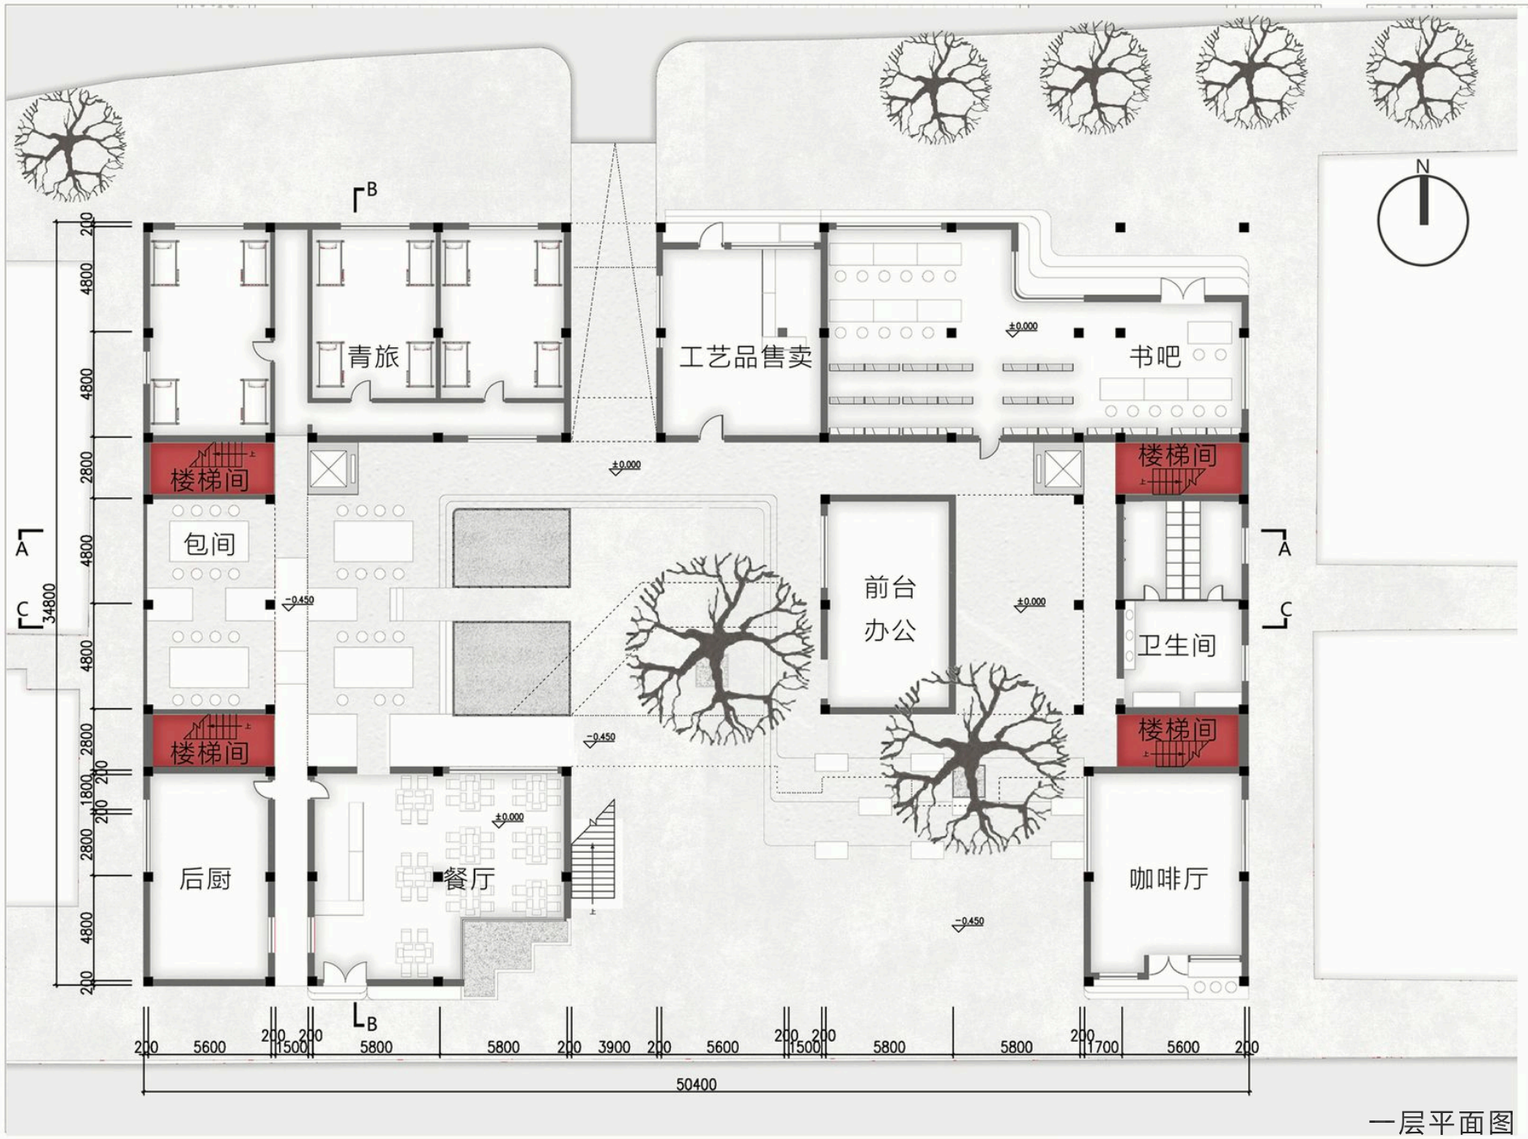

一层平面图

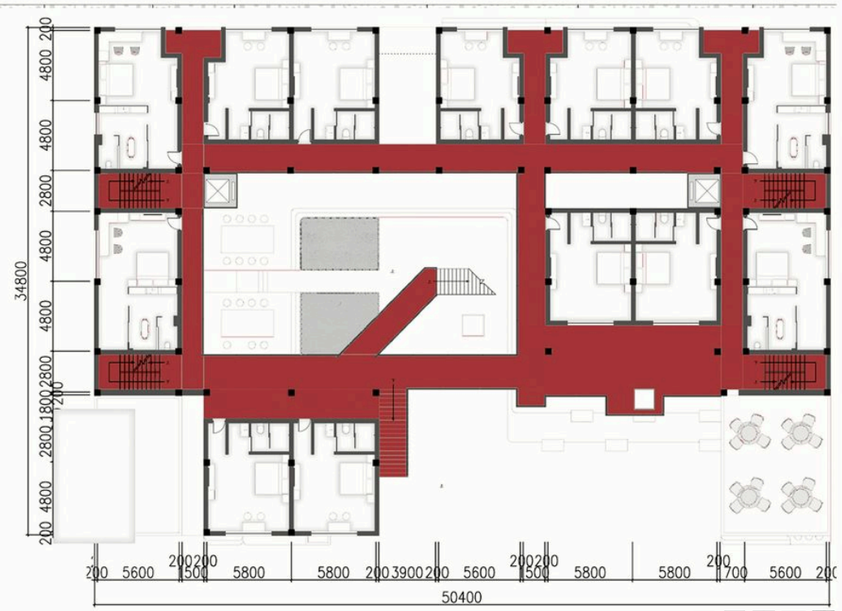


二层平面图





三层平面图





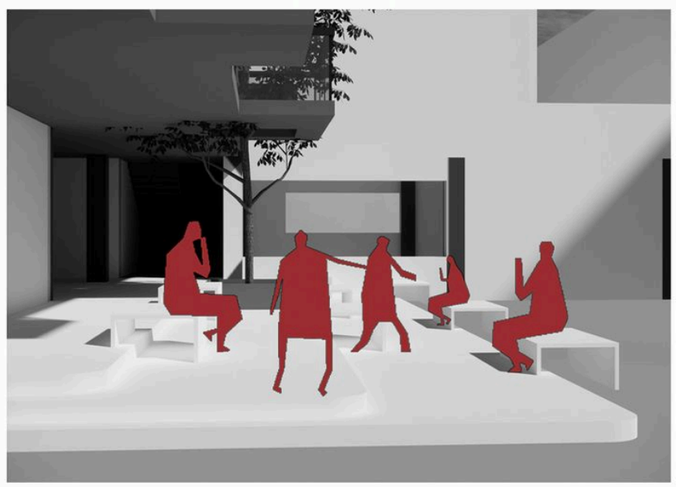

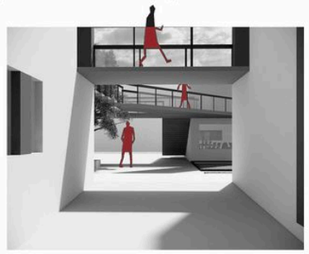

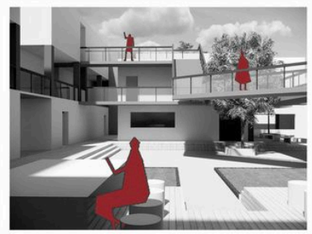







03

社区设计：板筑之间

传统版筑与现代运动叠合的全龄共享社区

2025.07

合作项目

地点：西安明城区西南隅冰窖巷，北向正对天主教堂

总用地面积：1.6公顷

总建筑面积：2.4公顷

类型：全龄友好运动社区（居住+体育配套）


“板筑之间”以传统“版筑”夯土技法为设计原点，将层层板片外廊结构转化为建筑语言，在底层与各层平台之间释放大面积的立体公共空间，构建全龄友好的运动社区。项目选址于冰窖巷地段，北向正对天主教堂，南接城市主干道甜水井街，步行可达含光门遗址、环城公园与小南门市场，兼具居住的便捷与私密，同时具备对外开放的潜力。设计以“运动+共享”为核心理念——板片如廊檐层层延伸，围合出通风良好、绿意盎然的半室外活动场所，涵盖200米环形跑道，超过500㎡集中室外活动场地、不小于2000㎡室内健身空间，以及篮球、羽毛球、乒乓球等多类型运动设施，满足少年嬉戏、中年解压、老年健体等多元人群的运动需求。








底层架空与板上平台叠合布置，融入图书阅览、共享阅读角、社区文化记忆墙等弹性功能，使公共空间在运动之外兼具文化厚度。户型配置涵盖60㎡以下公寓、60-90㎡两人之家、90-120㎡两代共居、120-144㎡三代共居等多种尺度，回应不同家庭结构的居住需求。绿化率超过30%，住宅屋顶绿化面积不小于屋顶总面积的50%。场地内将历史“冰窖”元素转译为铺装细节与节点空间，在传承古城文脉的同时，推动社区从封闭居住向开放共享转型。整体以“从土地中生长”的谦和姿态，实现传统版筑与现代健康生活方式的叠合共生。

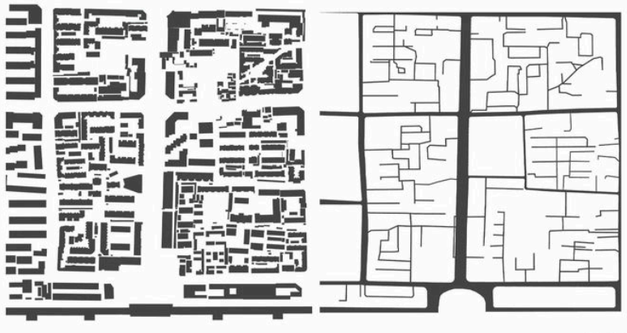

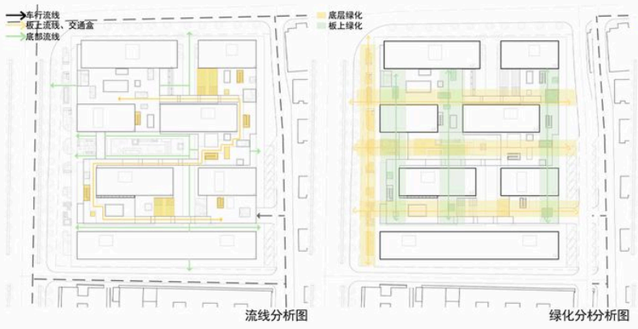


流线分析图

绿化分析图




无障碍分析图

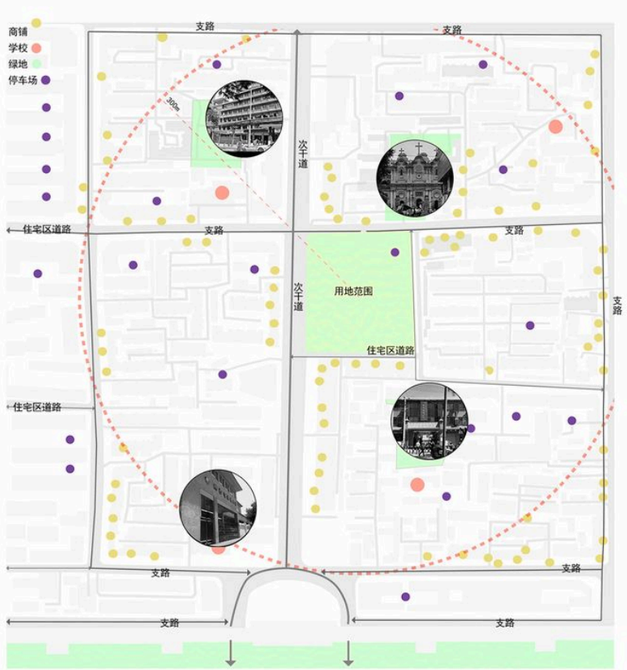

流线分析图

顶板

为保证安全屋顶采取女儿墙加护栏结构，

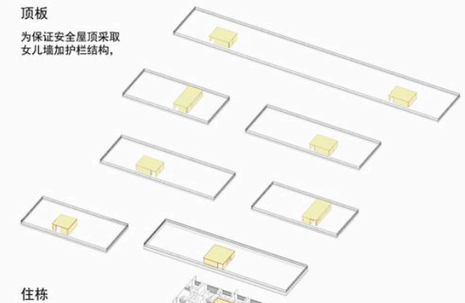


住栋

采取外廊式结构，灵活性强，视野开阔，南侧保证正隐私与采光，北侧保证通风采光。



结构

采取9600mm*9600mm钢制柱网，保证卧室的舒适度并增加富裕空间，工字梁钢框架结构在承载力和稳定性的前提下减少建筑成本。

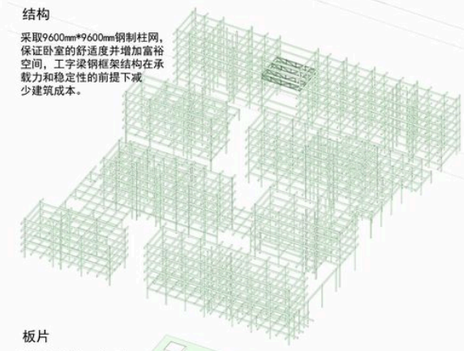

板片

钢制板片结构，施工快，刚度高，同时增加了空间的灵活性释放出大量的公共空间增加社区活力。



底层

充分利用底层空间，最大化激活街区活力与城市界面。充分的公共空间和运动空间促进邻里社交与社区凝聚力。



爆炸分析图




开放连接 · 共享生活

通过多层次的开放空间与共享平台，打造单一的居住模式，形成邻里互动、公共交流与自然融合的复合居住社区。



灵活共享 · 复合功能


室内外空间互通，公共活动区与居住单元有机合，满足学习、交流、休闲等多样化需求。

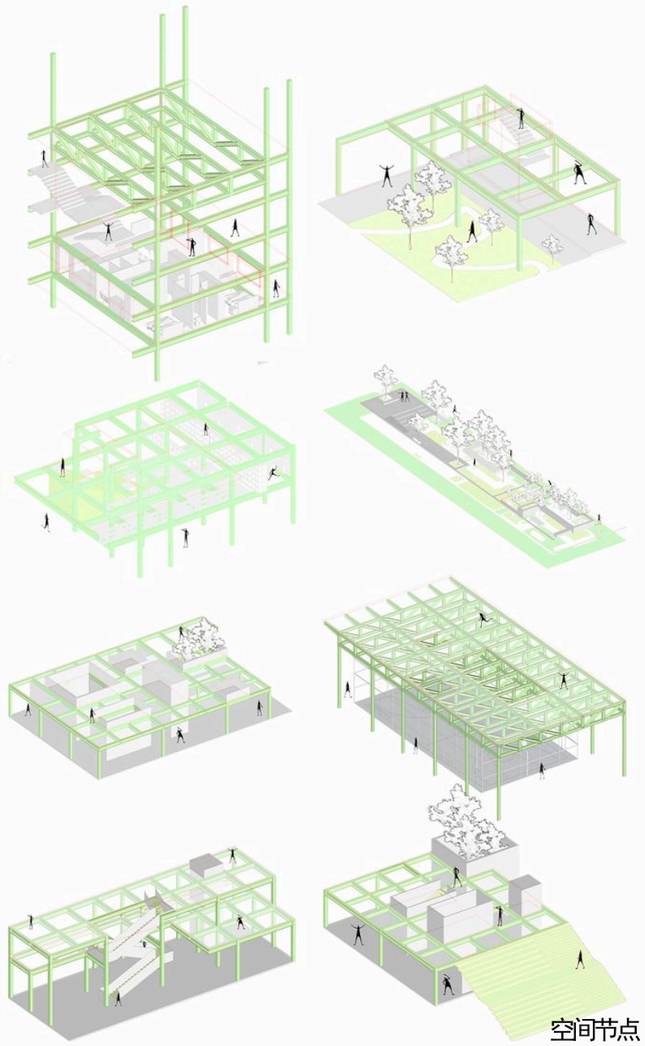

空间节点




总平面图

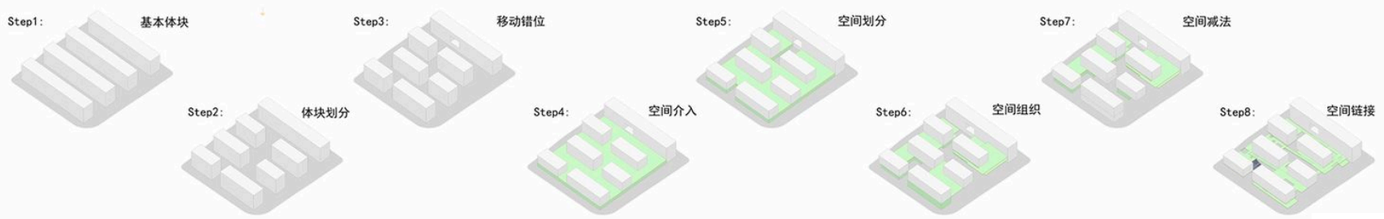

生成过程




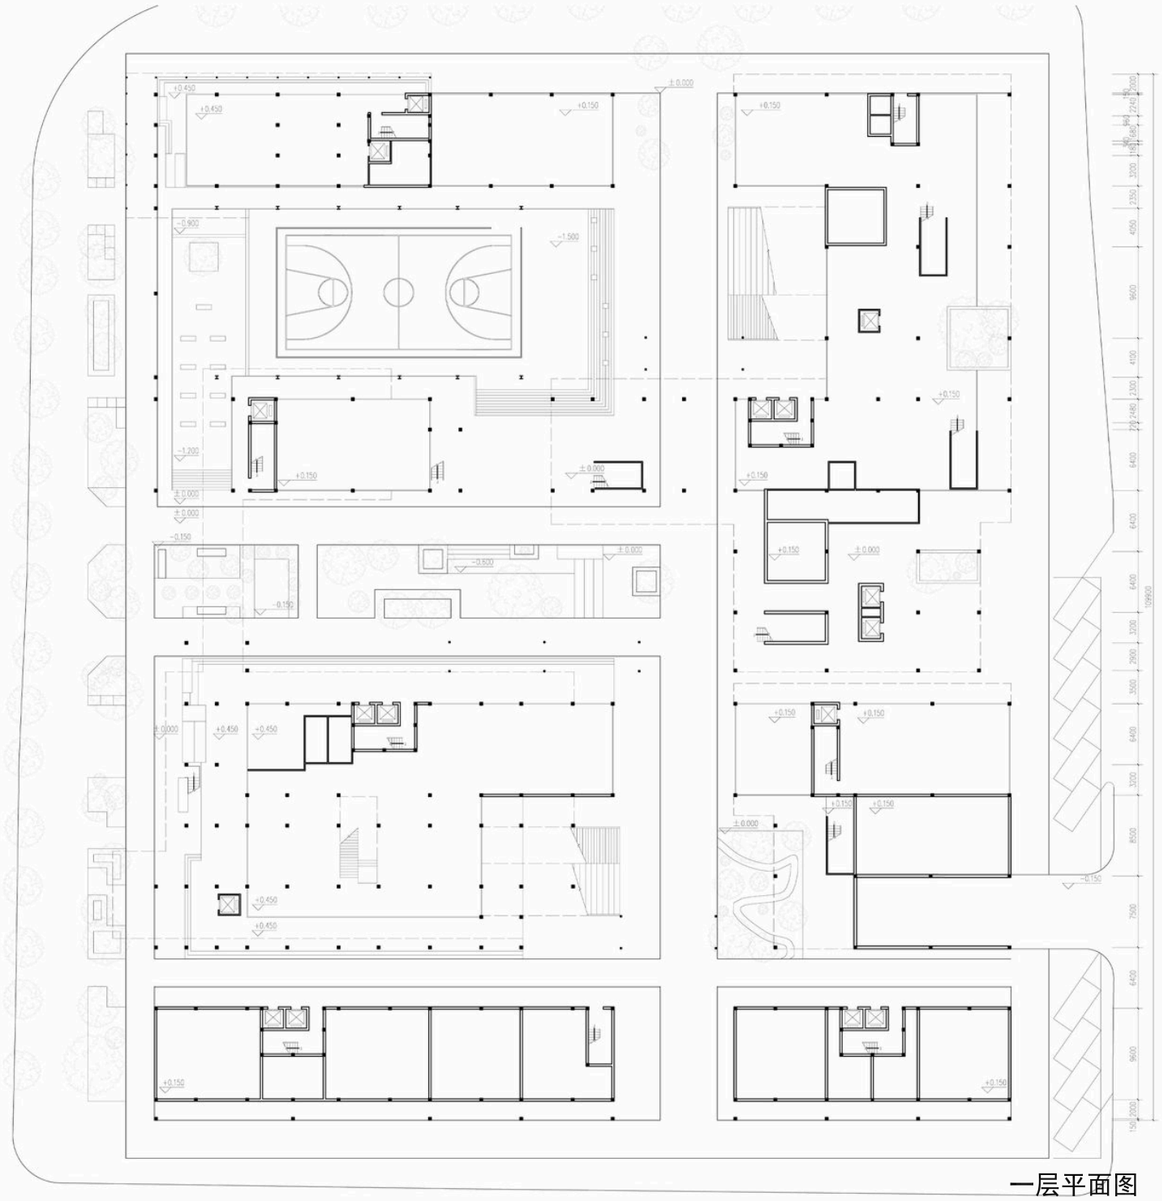


一层平面图




剖面A处人视图

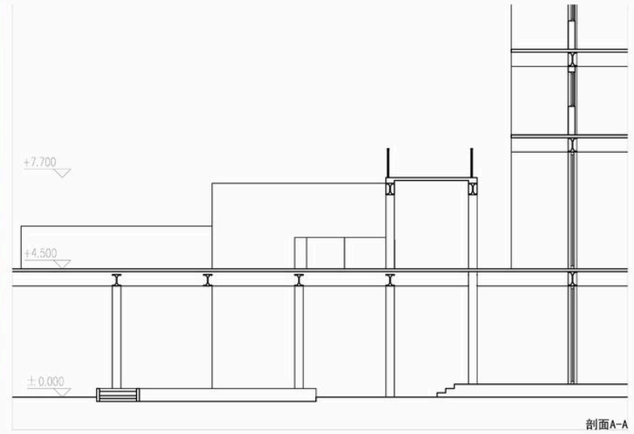


剖面A-A

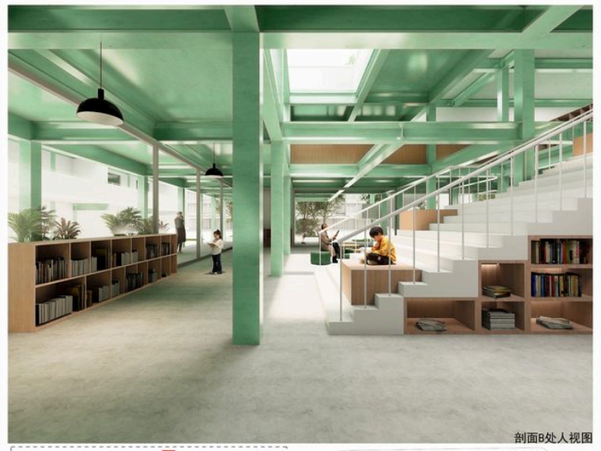

剖面B处人视图

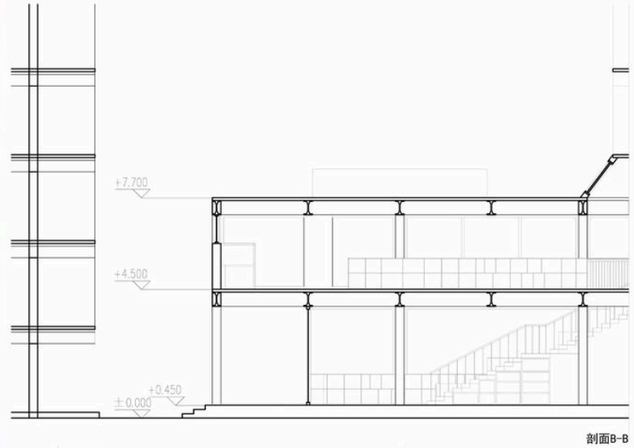


剖面B-B

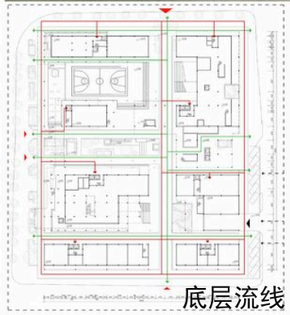

底层流线




底层功能

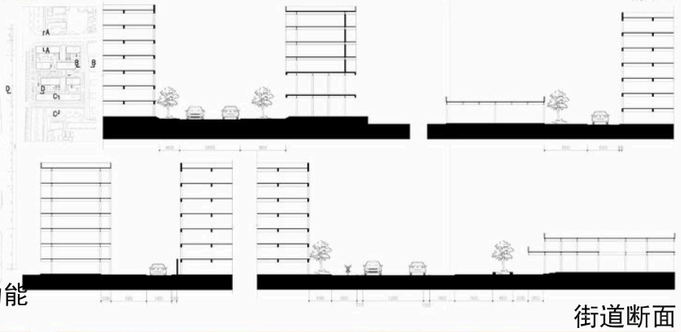


街道断面






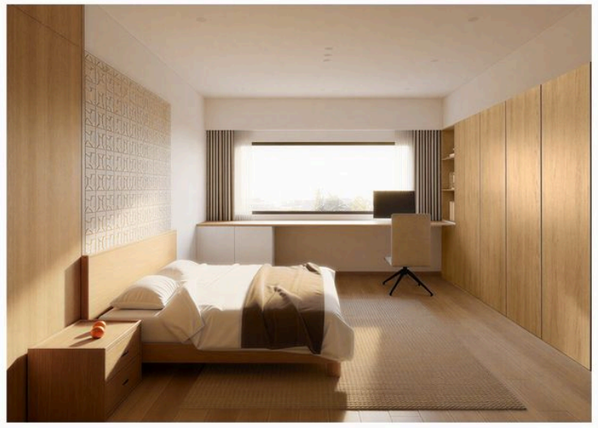


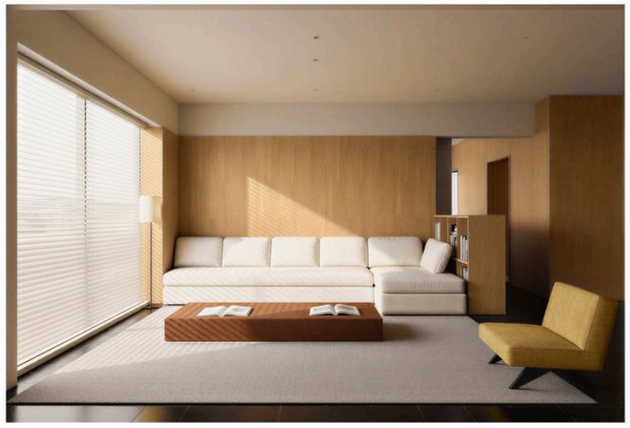



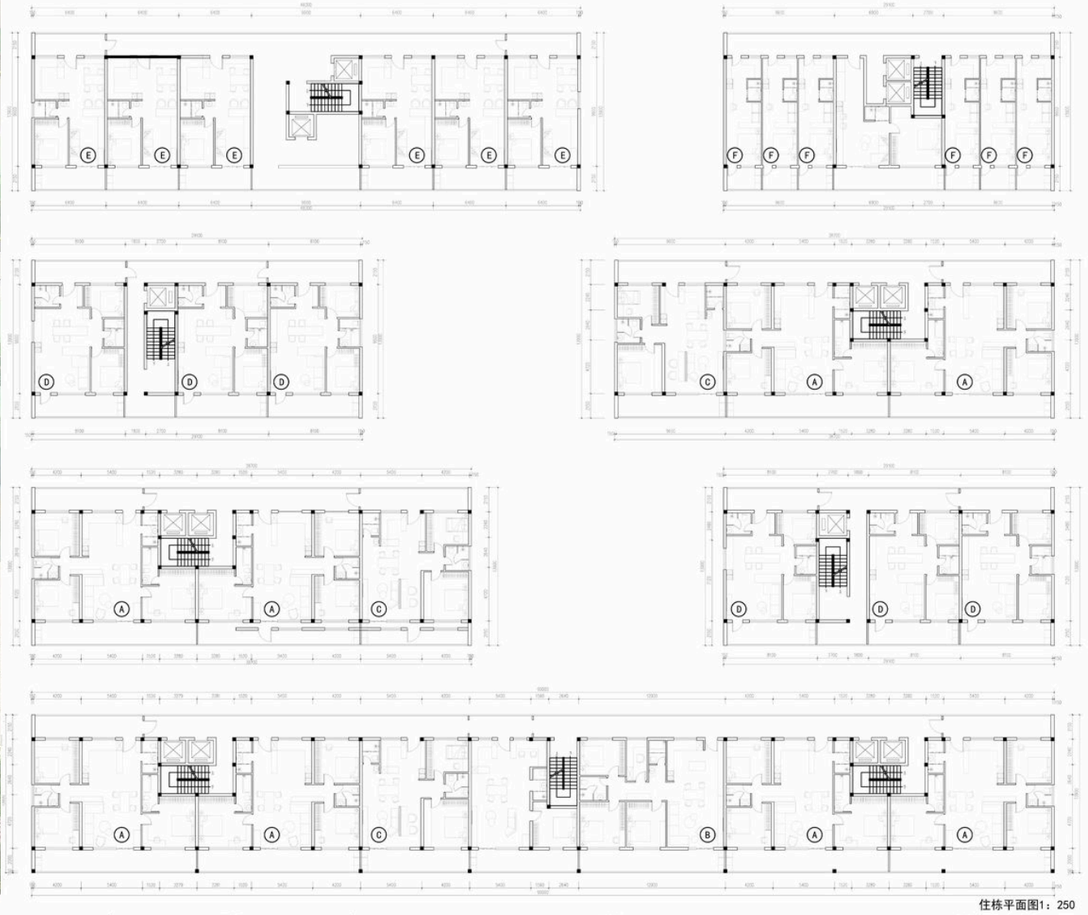

住栋平面图1：250

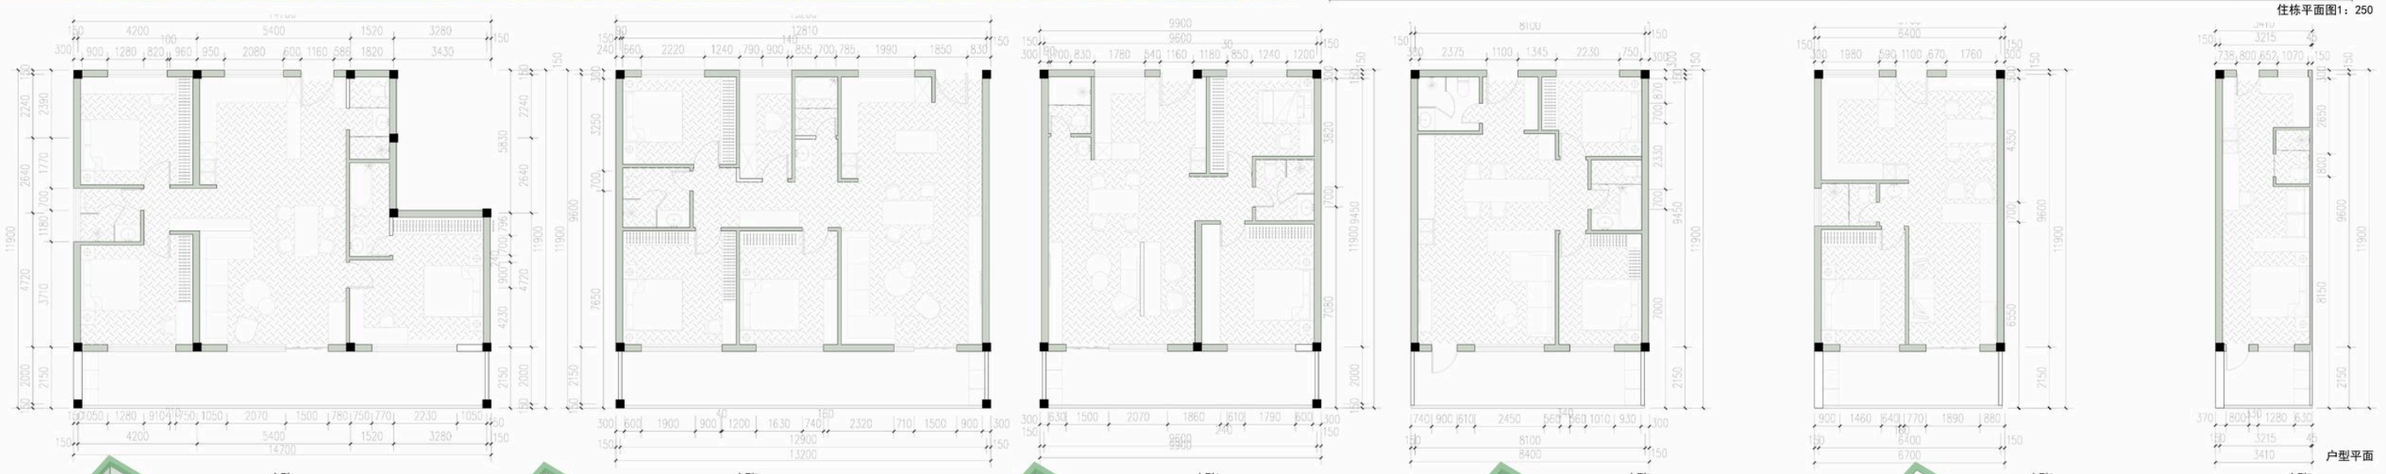

户型平面



户型A
总面积：145㎡
套内面积：130㎡
户型意象人群：中年夫妇及子女、父母

户型B
总面积：143㎡
套内面积：133㎡
户型意象人群：中年夫妇及子女、父母

户型C
总面积：108㎡
套内面积：96
户型意象人群：中年夫妇及子女、父母

户型D
总面积：92㎡
套内面积：82㎡
户型意象人群：中年夫妇及子女

户型E
总面积：73㎡
套内面积：67㎡
户型意象人群：中年夫妇

户型F
总面积：37㎡
套内面积：32
户型意象人群：暂住人群

户型轴测

04 片区设计：场域之间

基于形态研究的概念性城市设计

2026.09

合作项目

地点：西安卧龙禅寺片区

总建筑面积：6.1ha

类型：城市更新

设计说明：


卧龙寺片区位于西安老城核心区，历史积淀深厚，是城市重要的文化记忆锚点。然而，现状中卧龙寺被高耸的寺墙围合，与周边城市日常生活相互隔绝-一寺墙之内是静默的历史，寺墙之外是匆忙的穿行。周边街巷虽在，却退化为单纯的通道，不再容纳停留与交往;空间虽存，却难以支撑公共生活的发生。


纪念性建筑与城市日常彼此孤立，公共空间日渐失去活力。设计以“老西安人的会客厅”为核心理念，试图在历史与现实、纪念与日常、节庆与生活之间的“场域之间”，重新建立卧龙寺与城市日常的关联。





总平面图

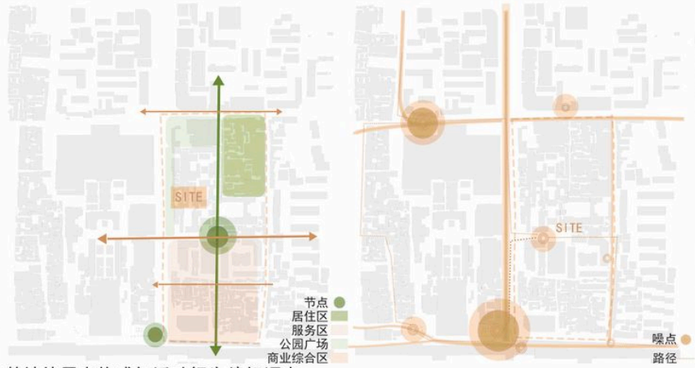


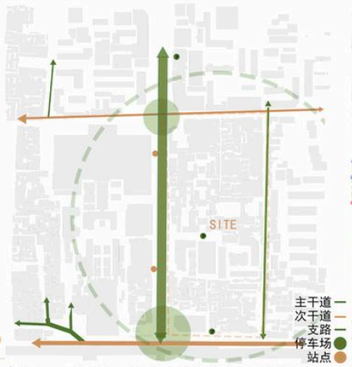




场地特征

基地使用者构成与活动行为偏好调查

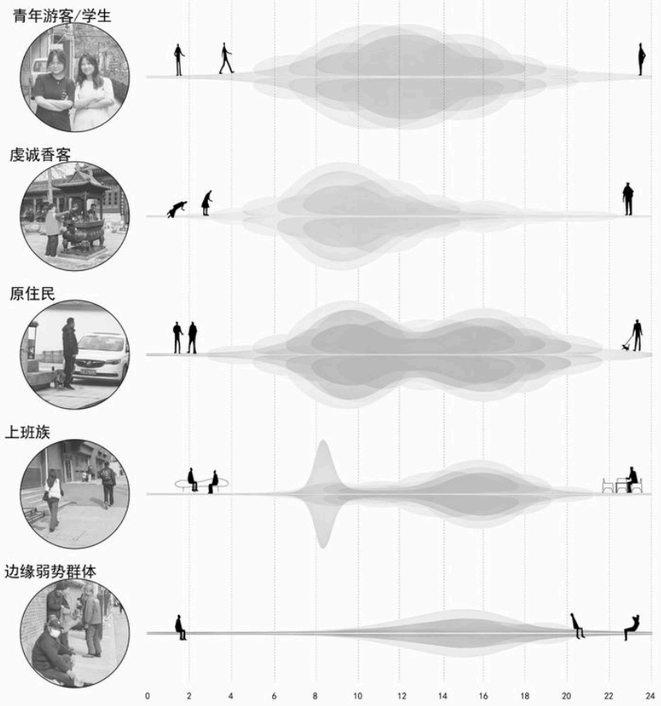

多群体需求、行为与情感交互矩阵

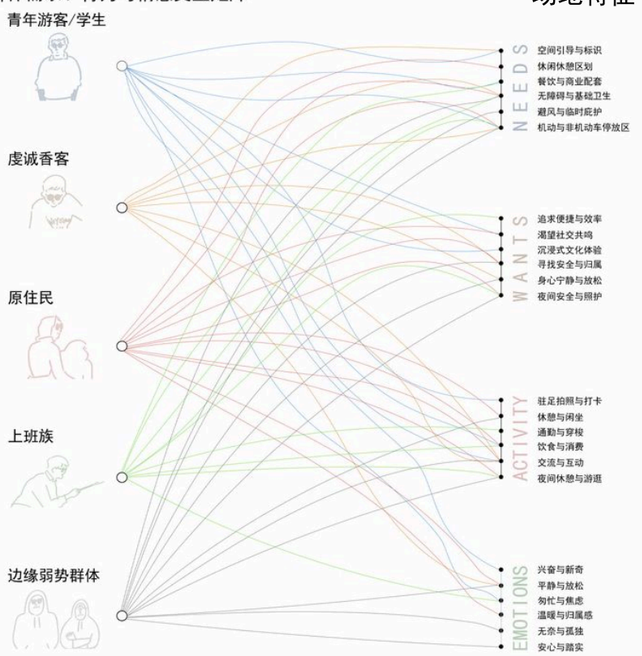


人群特征




街巷记忆


外来人群人群特质需求

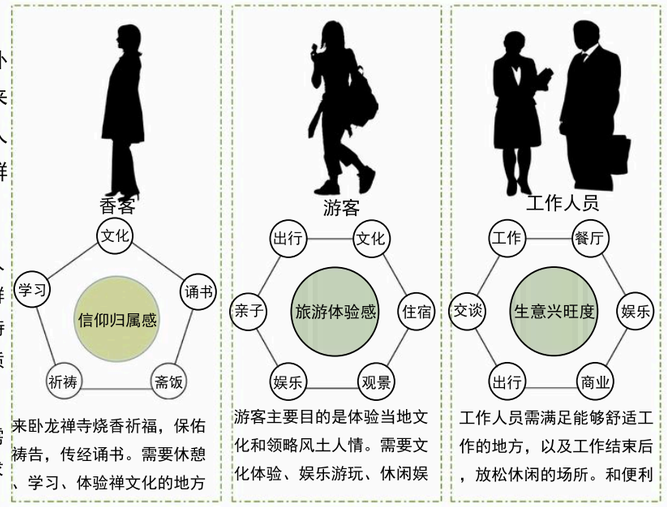

本地居民人群特质需求

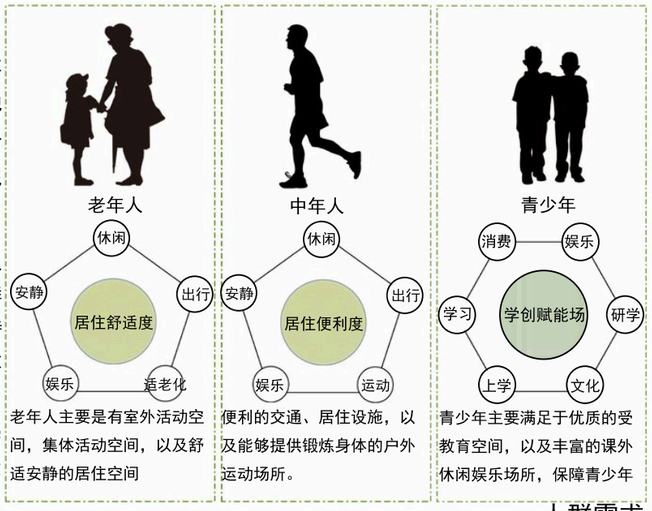

人群需求

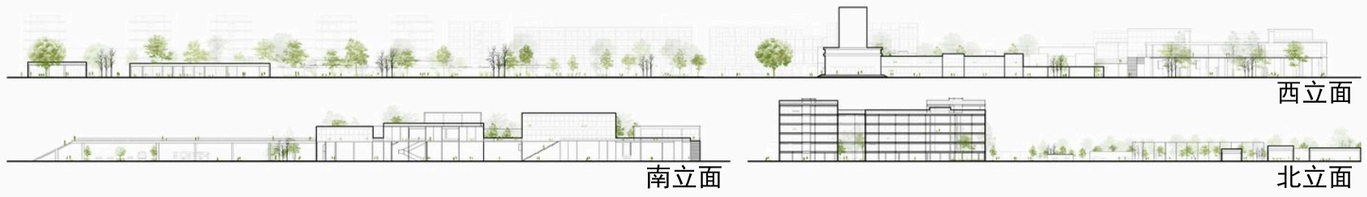

西立面

南立面

北立面

东立面



北街道断面


南街道断面



西街道断面




居住区建筑轴测

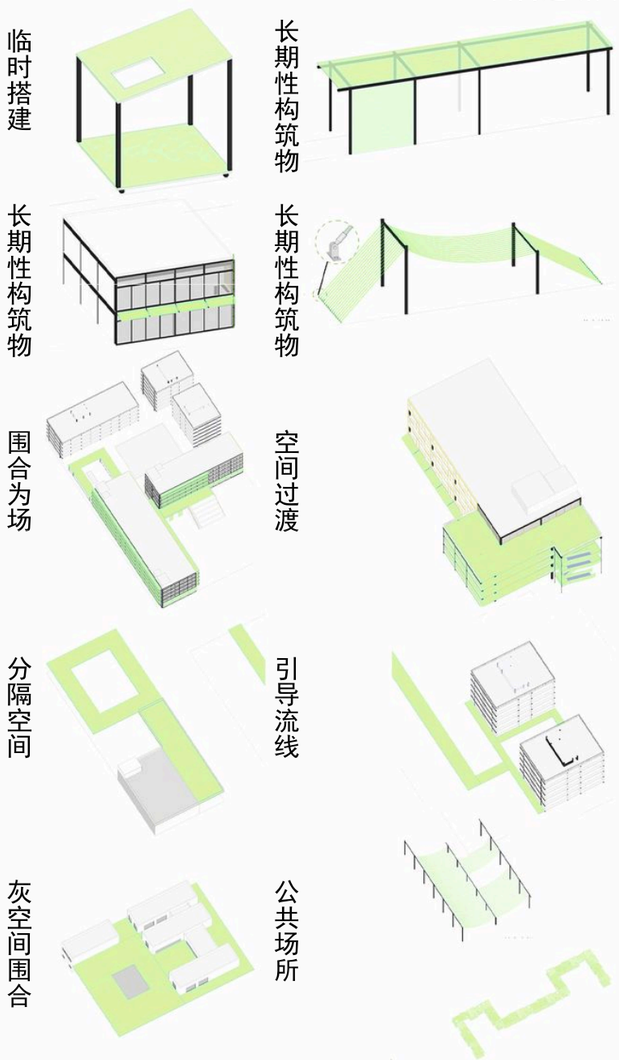



鸟瞰图

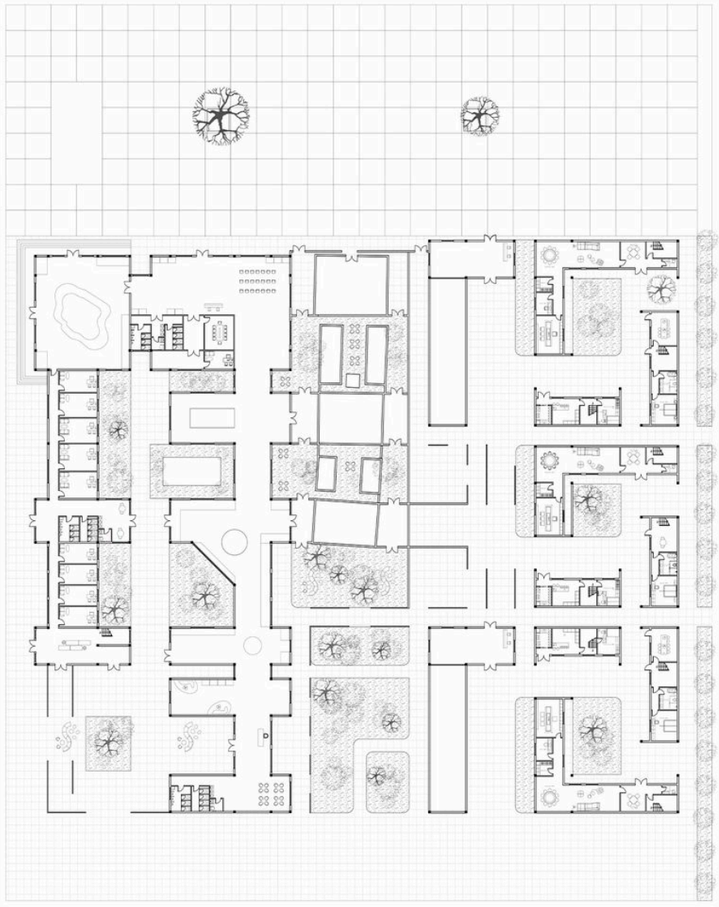




设计提出“场域、街、雨棚、活动”四重策略。以卧龙寺前文化广场为母本，向北生成城市公园，向东生成生活广场，向南生成节日广场，形成一场带三场”的空间骨架。


从卧龙寺前文化广场到生活广场、城市公园、节日广场，每一处节点都在类型转换中重新定义自身纪念性建筑向城市敞开，服务性空间向社区共享，商业设施向公共生活让渡界面。设计回应了"开放共享”的时代诉求，也回应了西安老城对公共生活的期待。它不是一座建筑，而是套让公共生活重新发生的空间系统在场域中相遇，在街道中连接，在雨棚下停留。






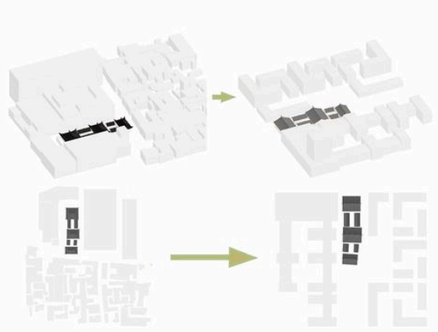





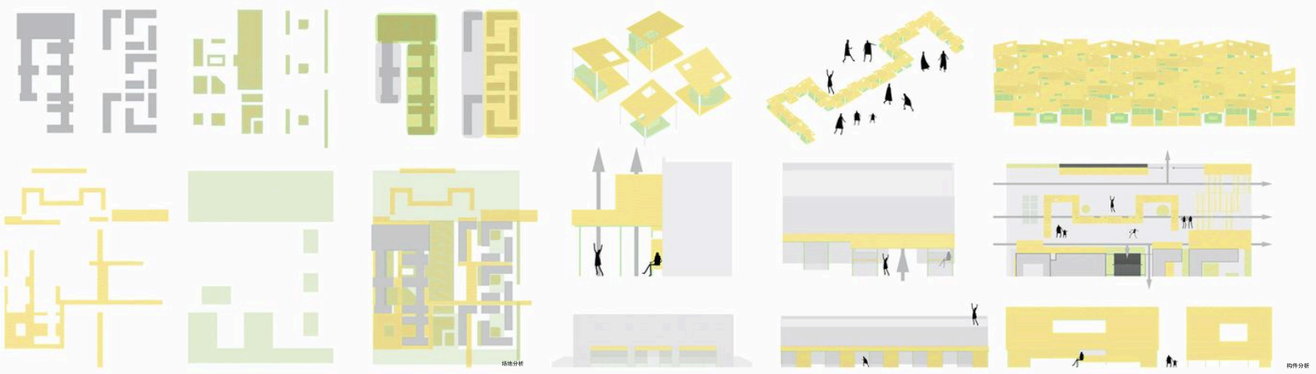


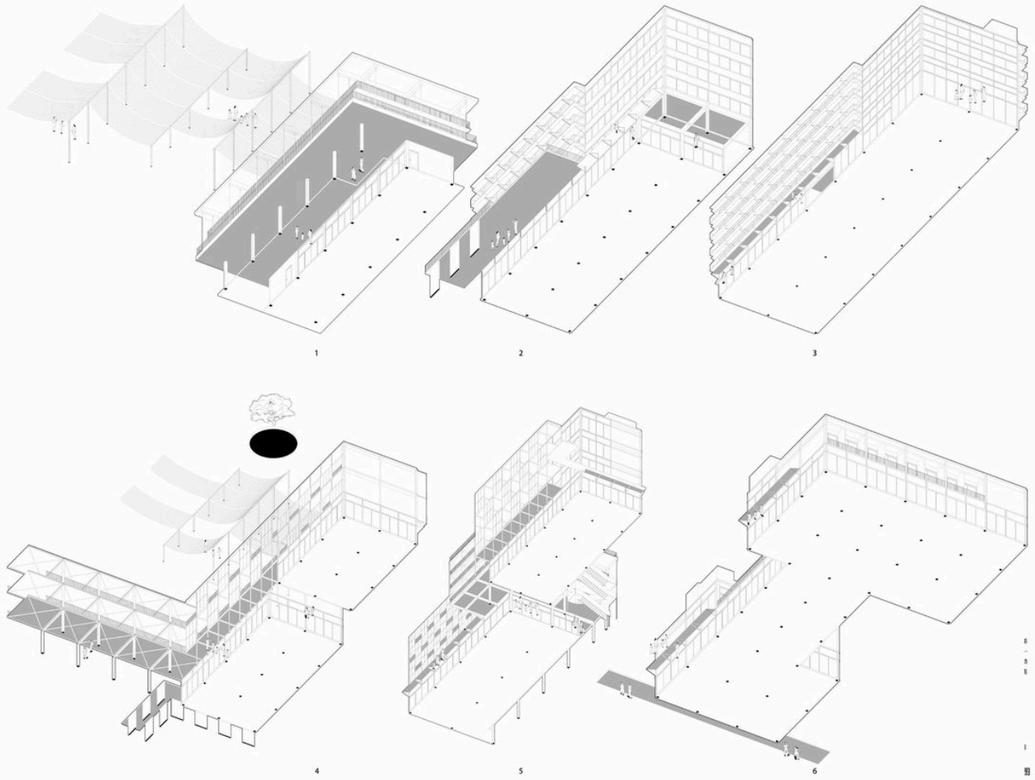

以城市形态学、建筑类型学为理论工具，通过“含义”与“结构”的双重转换，回应公共生活的重建需求。
类型含义多义化—在“含义”层面打破封闭的单义指向。让建筑形式向城市语境开放，创造与公众的直接对话;同时容纳多元解读，鼓励公众按照不同的理解使用空间。形式不再是固定的“纪念性”或“功能性”，而是具有多重释义可能性的公共容器。类型结构自由化-—在“结构”层面突破僵化的空间等级。让建筑空间与城市结构高度连通，消除界面障碍，确保公众可自由穿行;同时预设灵活可变的内部空间结构，以适配多元化的公共生活需求。空间不再是被动的“房间”，而是主动适配活动的弹性场域。

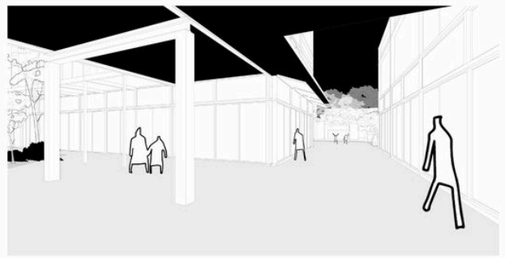

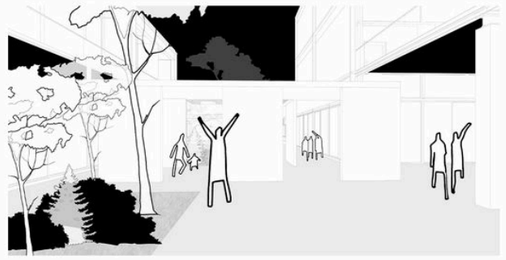

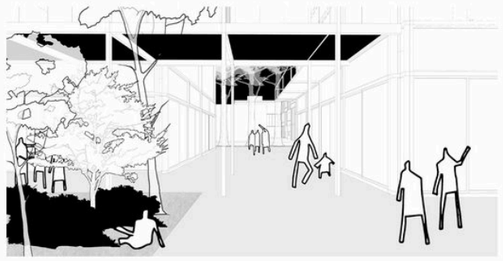











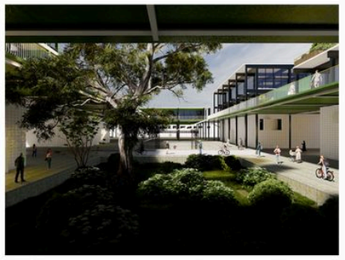







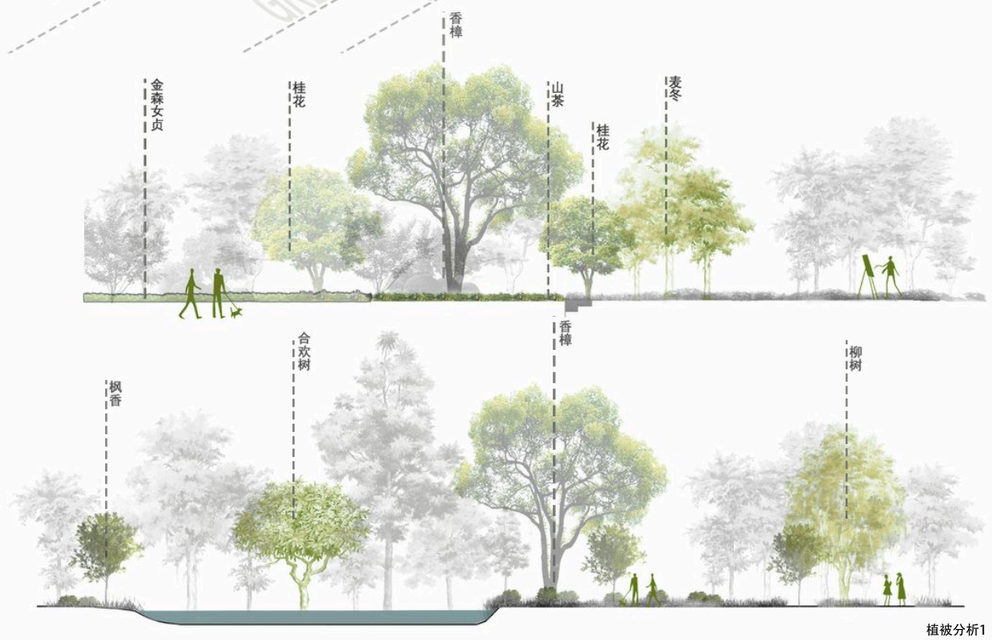

植被分析1

05 驻场实践：咖啡店

商业空间改造的现场配合与图纸复核

店名：Second Half下半场

2026.10-2026.01

耕精伫工作室驻场建筑师

地点：西安城墙内湘子苗街门口

类型：商业空间改造

整体介绍：

Second Hlaf南门店是一处临街商业空间的整体改造：砸除原地面、搭钢架吊顶、砌砖墙、布水电，再做吧台与室外卡座。结构、水电、面材的界面互相牵扯，图纸上的一条线，到现场往往要先争出十公分的余地。

南门店前后做了三个月，我一共进场六十余次，写下四十余份施工日志。做的事很具体：进场先复核尺寸，把偏差写回 CAD；指出做错的地方，与设计和施工方当场定处理办法；把当天的进度、量到的数据、没解决的问题写下来，作为下一次进场的依据。



图纸与现场

把现场量回图纸

十月二十日进现场复尺，吧台的进深比图纸上大得多：北侧柱子的南边界到汉庭外立面 3840mm，拐角到外立面 12722mm，比原图多出约 300mm。台面厂家要按实测下料，图纸上这 300 的差，就是一块板报废。

于是把柱距、柱到厨房南墙、北边界到柱一并量回，重排吧台放线。此后的图纸改动，大多从这个尺寸开始。

实测数据 · 2025.10.20

柱北边界 → 汉庭外立面	**3840**
拐角总进深（较原图 +300）	**12722**
柱子南北进深	**530**
柱 → 厨房南墙	**1840**
北边界 → 柱	**850**

量完之后，图纸上跟着改的六处

10.20 **吧台放线与外围台阶复尺**

进深按 3840 / 12722 重排；柱距 530、柱到厨房南墙 1840、北边界到柱 850 一并量回，供台面厂家下料。

11.27 **CAD 补两台设备**

吧台缺一台热水宝、一台拼豆机；冷萃机从后厨移到吧台，水电点位随之下移。

12.03 **吧台上方管线改位**

南侧进排水管原位置会顶住台下机器，改走台面上方，复查记录“位置更改完成”。

12.05 **喷淋头改位**


喷淋头更改完成，赶在吊顶封板之前做完，避免封板后二次开孔。

12.08 **卡座插座由五改三**


同步改水电点位；音响位置须在刮腻子前确定，留出开孔条件。

12.16 **门与台面的收口**


门改天地轴朝外开，西侧 40 不锈钢立柱留槽夹玻璃；台面上方不锈钢分为四块。

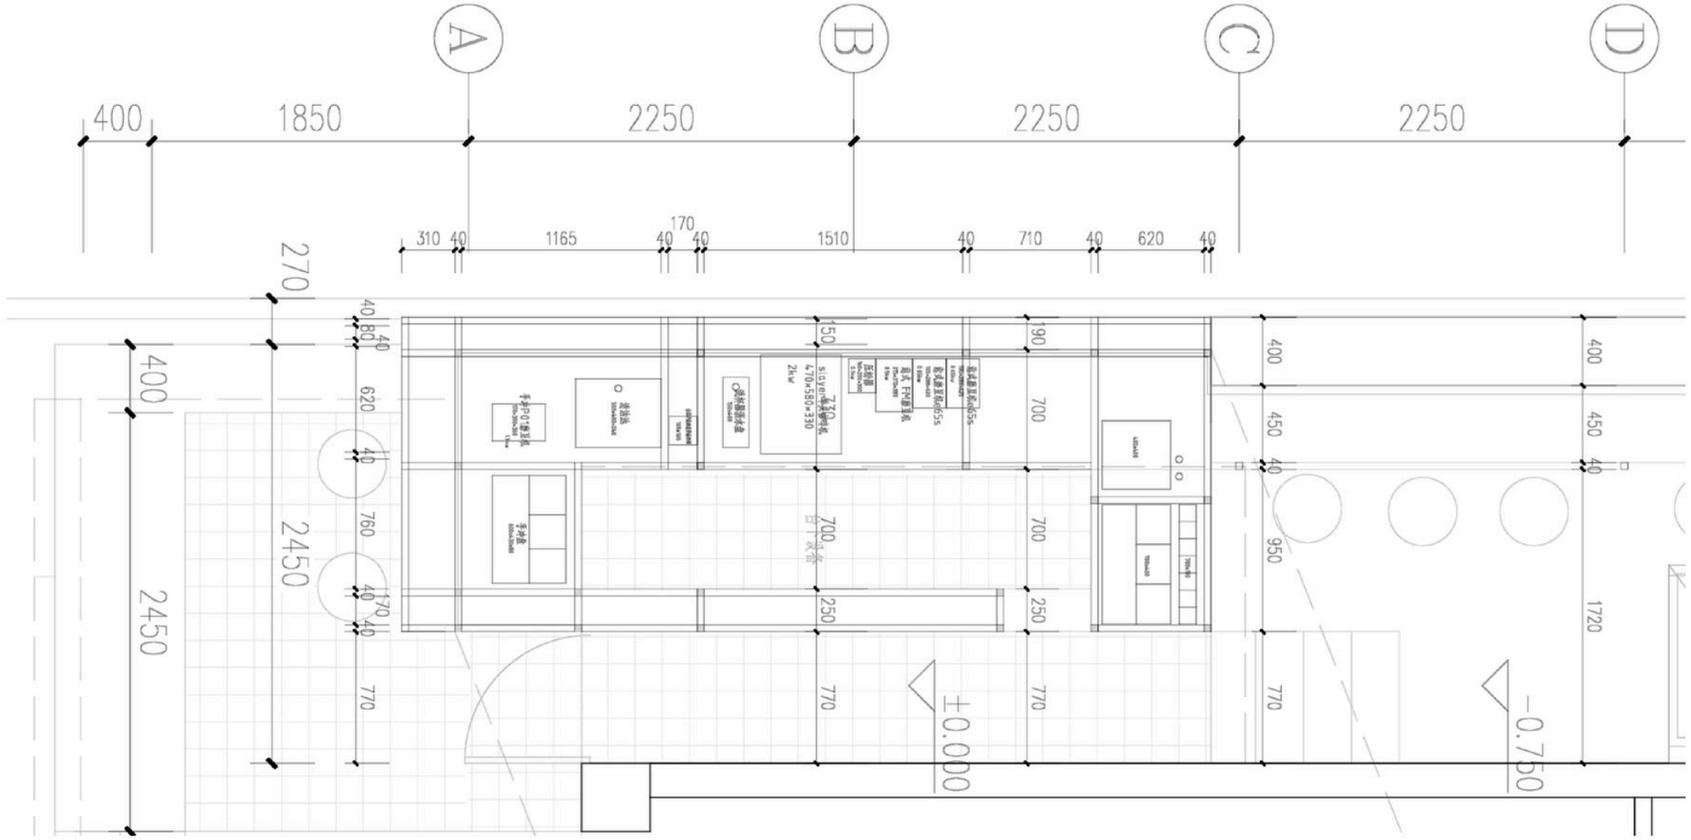

吧台平面（A—D 轴段；D 轴以东为整体空间，超出图幅）：柱位、台面板分段与外沿尺寸，2025.10.22 核对后施工图，单位 mm

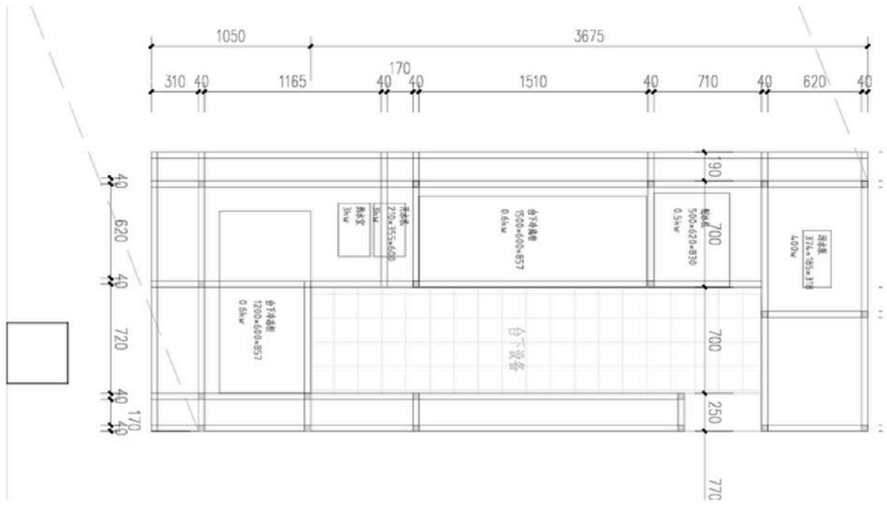

台面分段：按实测重排的分块尺寸与设备定位

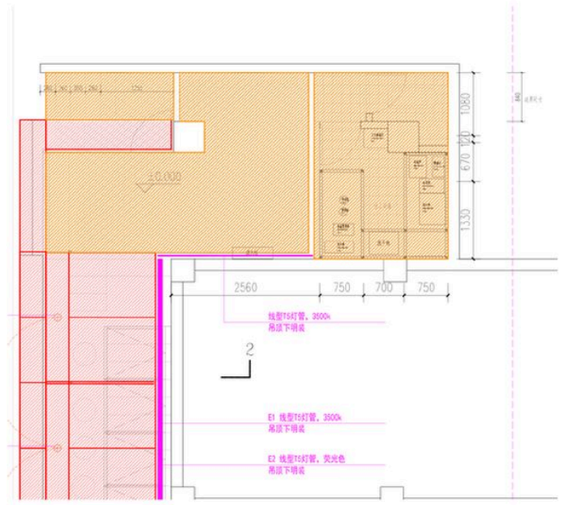

灯位与插座点位（不含空调、监控、音响）

2025.10.20 · 小雨

“吧台的尺寸比想象中进深大了一点……从拐角到汉庭外立面的总进深为 12722mm，比之前大了 300mm 左右。”

2025.11.27 · 晴

“吧台 CAD 中缺少一台热水宝和一台拼豆机器。”——当晚补图，冷萃机从后厨移到吧台，水电点位一并重排。

施工日志

六十余次进场

每份日志固定三栏：施工进度（谁在做什么）、情况记录（今天量到什么、看到什么）、待解决问题（谁负责、卡在哪）。工序一旦错位，靠这三行就能追回去。

南门店前后做了三个月，我进场六十余次，写下四十余份施工日志。这一页从里面挑出八天按时间排开，再挑出六件当场判定的事。



2025.12.03　工人用靠尺校墙面垂直，正在安装东侧墙面框架



3 个月
2025.10 — 12

60+ 次进场
三个月平均每周四到五次

40+ 份施工日志
当天写全，不补记

8 天摘录
本页所选

10.20　小雨
钢架吊顶完成数品，地面未砸完。实测吧台进深 3840，比原图大约 300。
待解决　北墙位置与砌块材料未定，需甲方拍板。

11.12　多云
吧台与吊顶框架搭建完毕；东侧墙面瓷砖、地下室最内侧墙完成。
待解决　北侧分界砖墙的砖块选择与摆放方式。

11.19　晴
楼梯口钢架完成，北侧入口模板拆除；南侧东墙做法有误，已与设计沟通解决。
待解决　咖啡厅柱子开不了槽、厨房新砌墙的开槽办法。

11.27　晴
北侧入口墙砌筑完成，吧台进水管与排水管就位；南侧水管位置错，会挡设备。
待解决　北墙加高尺寸、冷萃机移到吧台后的水电点位。

12.03　晴
电线布管初步完成，预留插座与开关；2500 吊顶框架基本完成。
待解决　开关插座到场后安装；每日收工必须切断电源。

12.05　晴
喷淋头改位完成；工人给吊顶钢架钉木条，为封石膏板做准备。
待解决　吧台插座采购，多买几个插口给热水保留位。

12.08　阴
吊顶石膏板基本装完；定下砖墙错缝与水管避让做法，卡座插座改为三个。
待解决　音响位置须在刮腻子之前确定，以便开孔。

12.16　晴
吧台与室外卡座砖砌基本完成；定门天地轴朝向与不锈钢留槽，进入抹灰上漆。
待解决　12.17 测量并确定窗户尺寸。

六件事，六次判定

问题	现场情况	判定与处理
01 **吧台进深与图纸不符**	实测 3840，比原图多约 300，台面无法按原图下料	重取柱距重排放线，实测值写回 CAD
02 **吧台下方水管挡设备**	进水与排水管顶住台下机器，设备放不进去	现场定改管路径，管线移到吧台上方
03 **北侧砖墙与水管抢位**	水管高过竖砖，内侧未预留砖宽，灰缝对不齐	水管下压，先内薄砖再外砖，灰缝求同高
04 **卡座插座数量偏多**	北侧卡座原设五个，现场判断不需这么多	核减为三个，同步改水电点位
05 **音响开孔来不及**	位置一直未定，吊顶已封板，再晚就要二次开孔	要求刮腻子前定位置，留出开孔条件
06 **门与玻璃的收口**	门改天地轴朝外开，西侧立柱要能夹住玻璃	定 40 不锈钢立柱并留槽，厂家据此下料